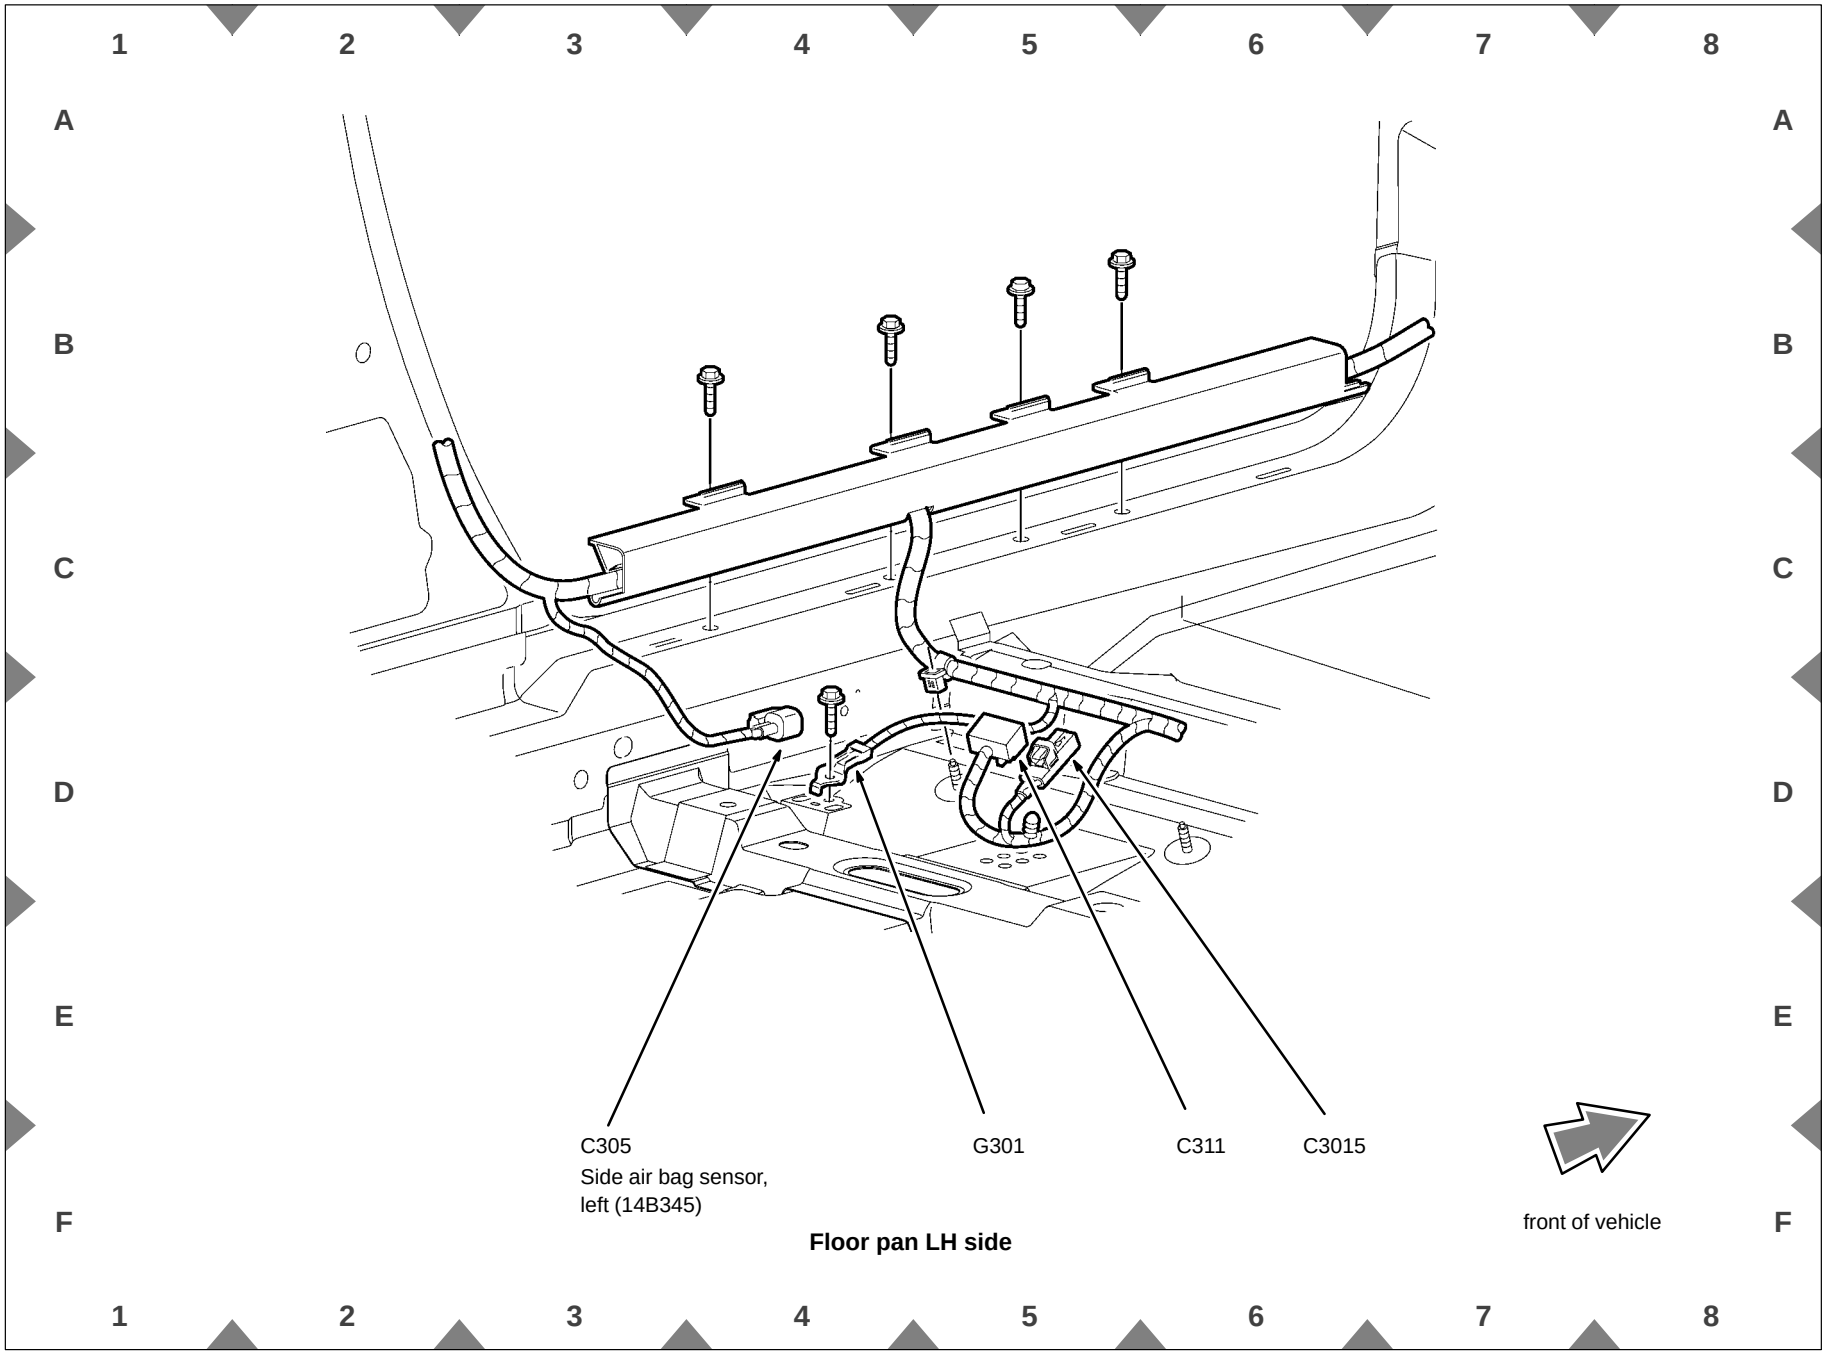

Floor pan LH side