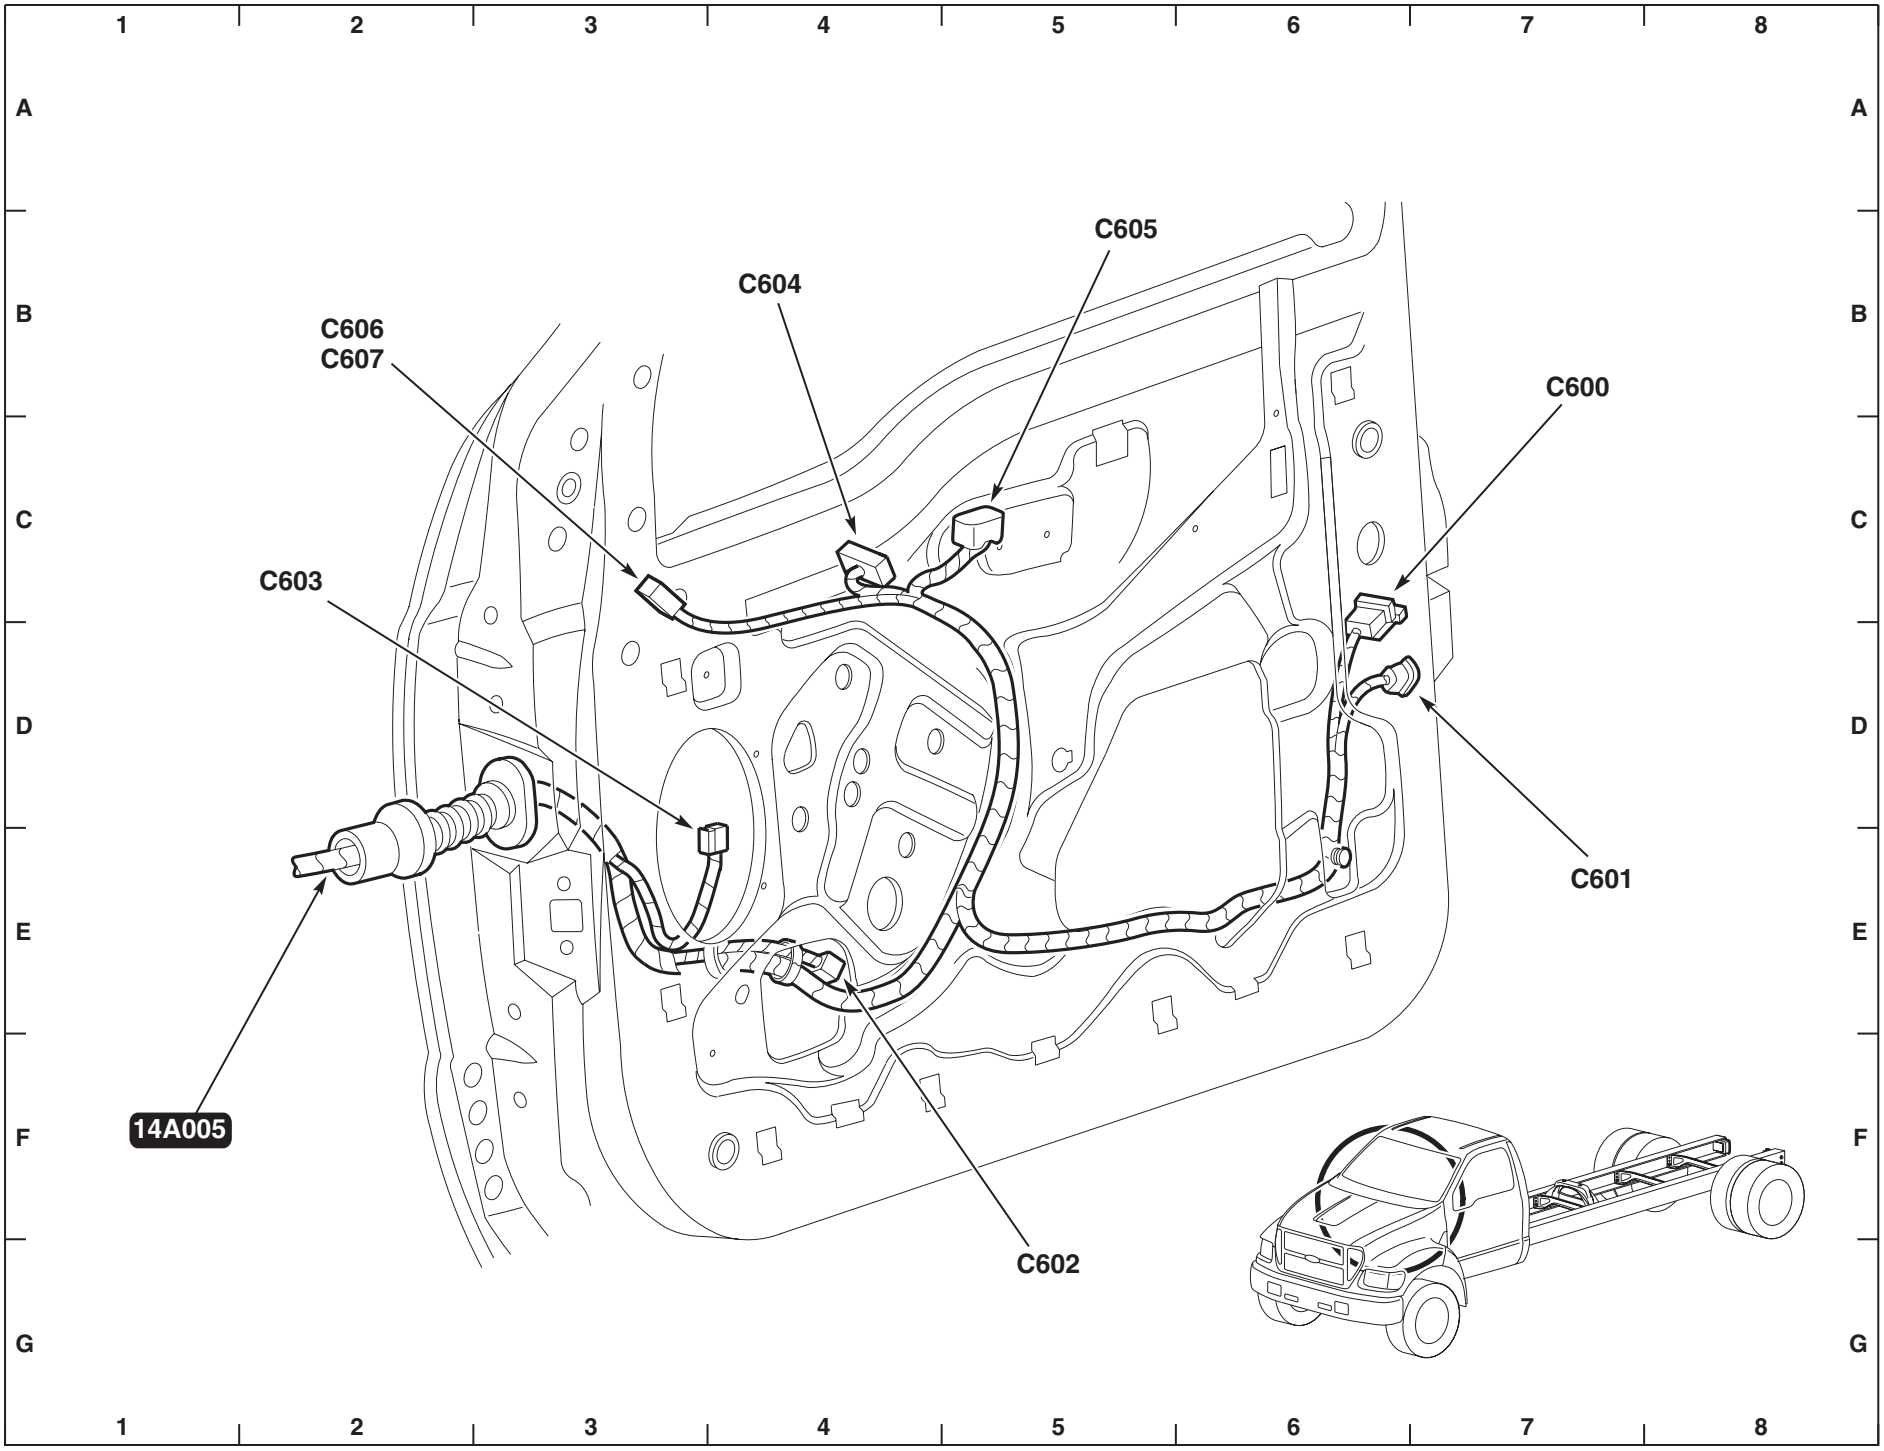


Right Front Door