REVISED
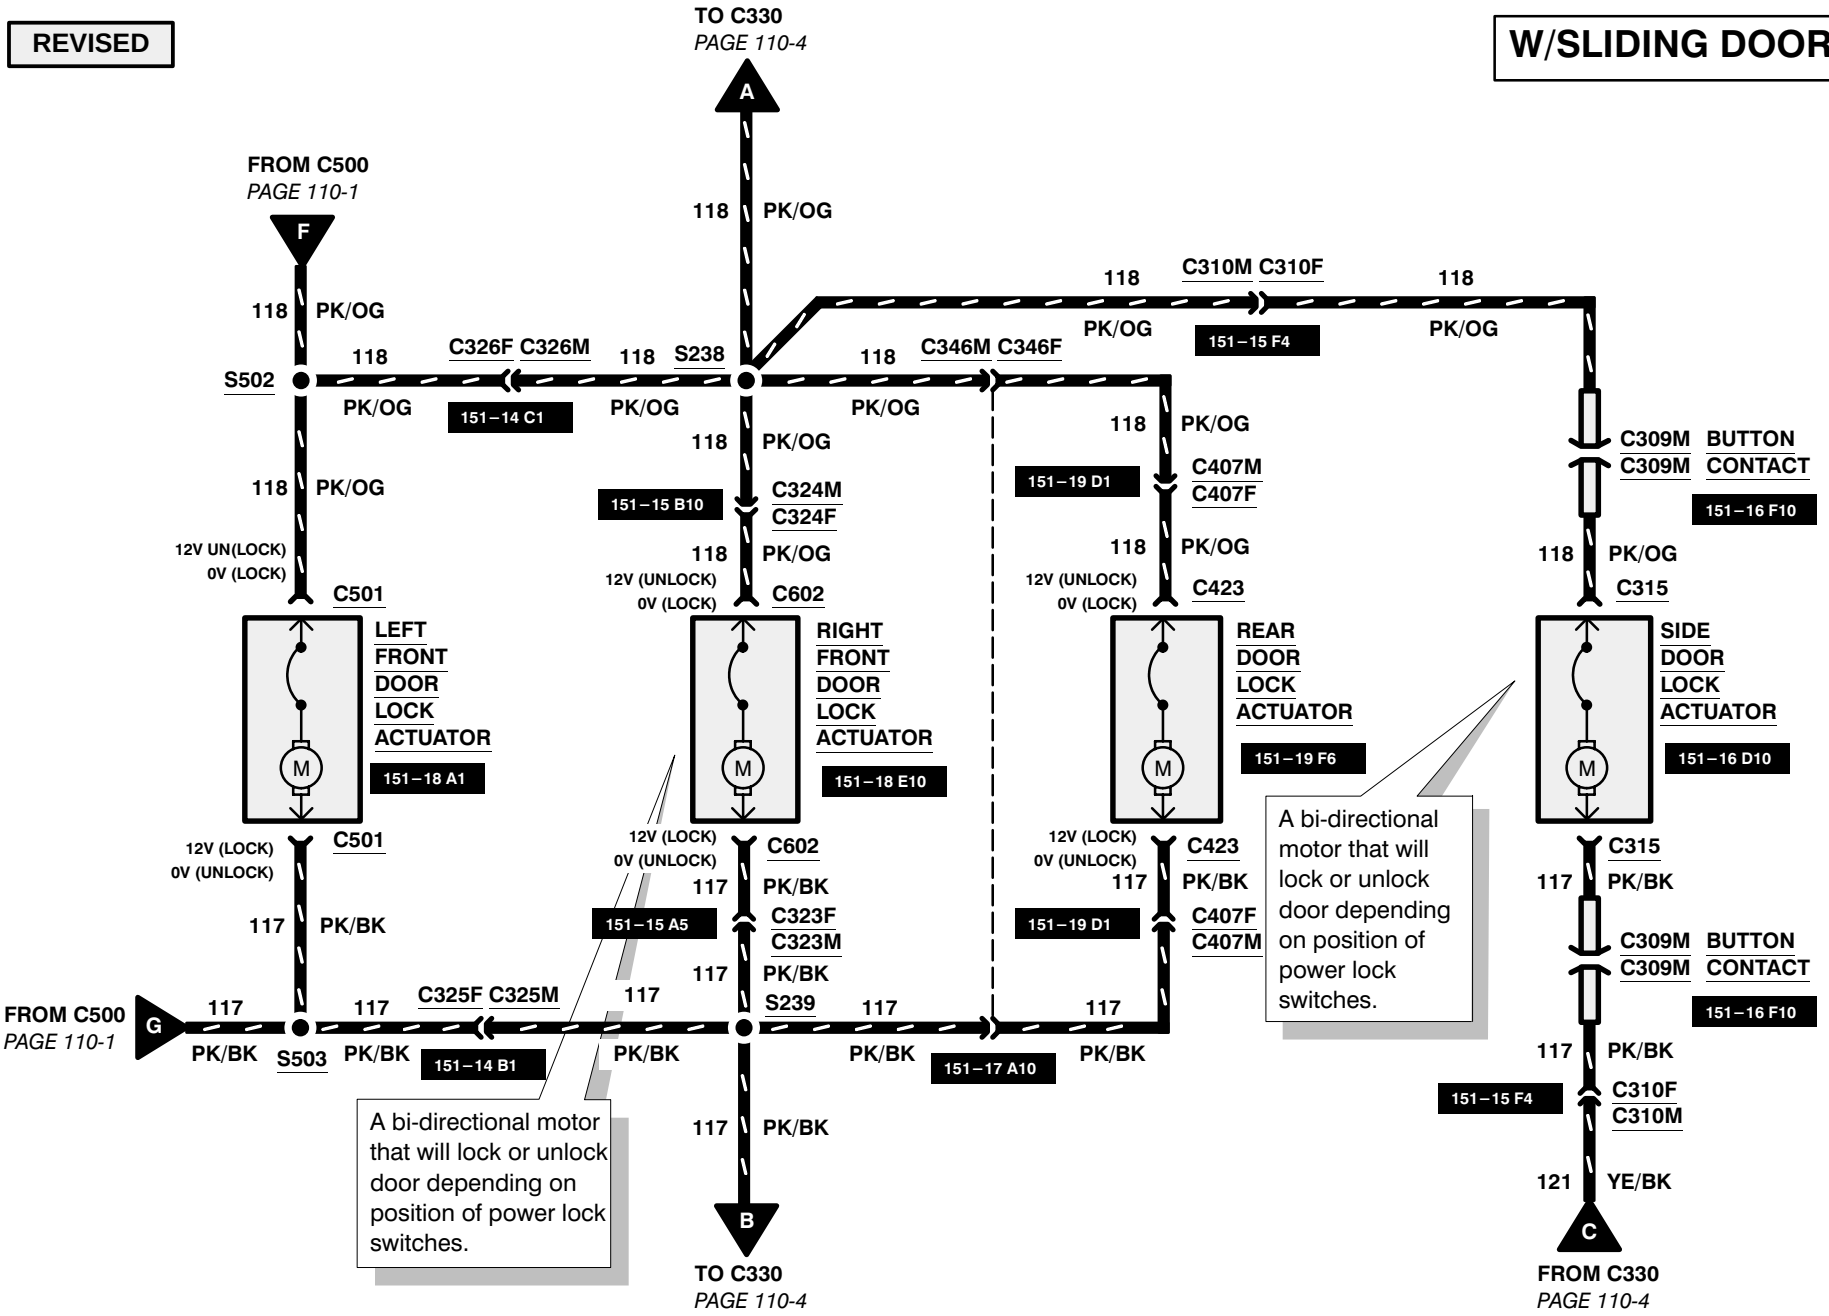
W/SLIDING DOOR