TERMINALS

SCHEMATIC

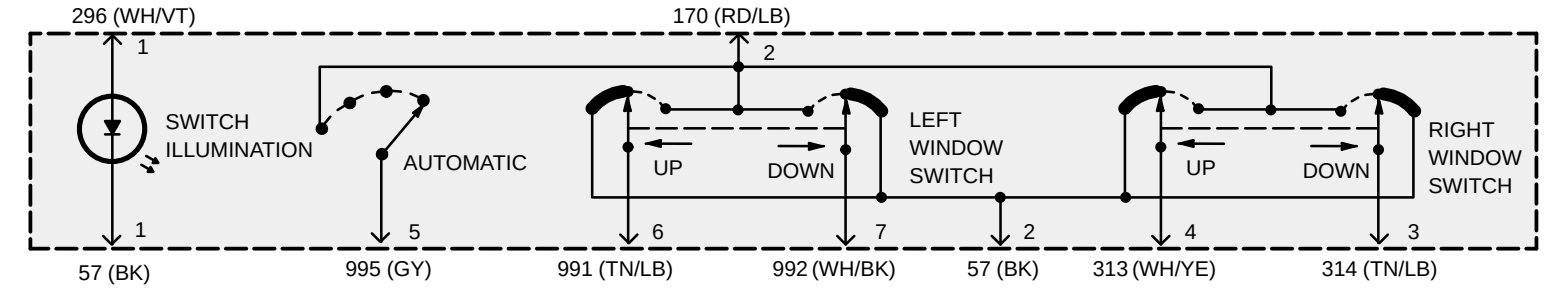

(FRONT WINDOW CONTROL SWITCHES)

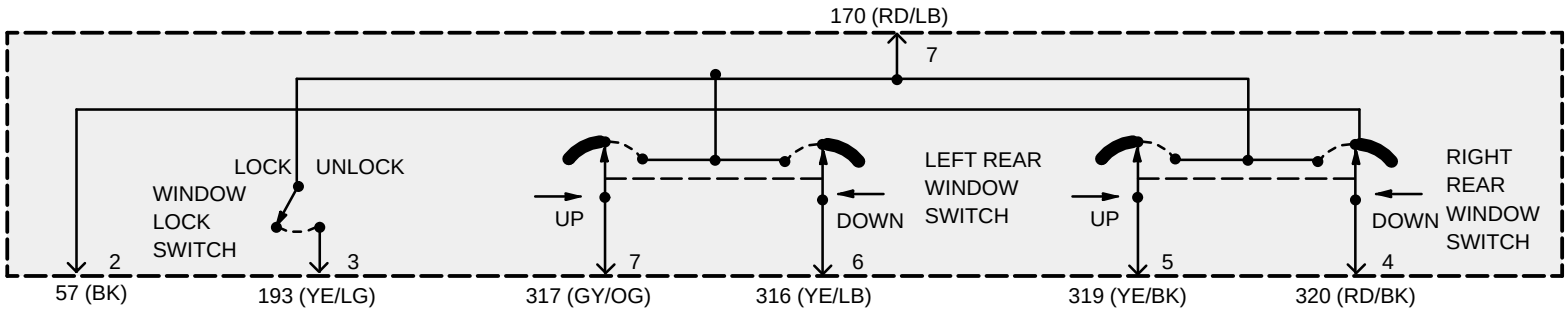

(REAR WINDOW CONTROL SWITCHES)