Master window/door lock/unlock switch – front and rear power windows

Schematic

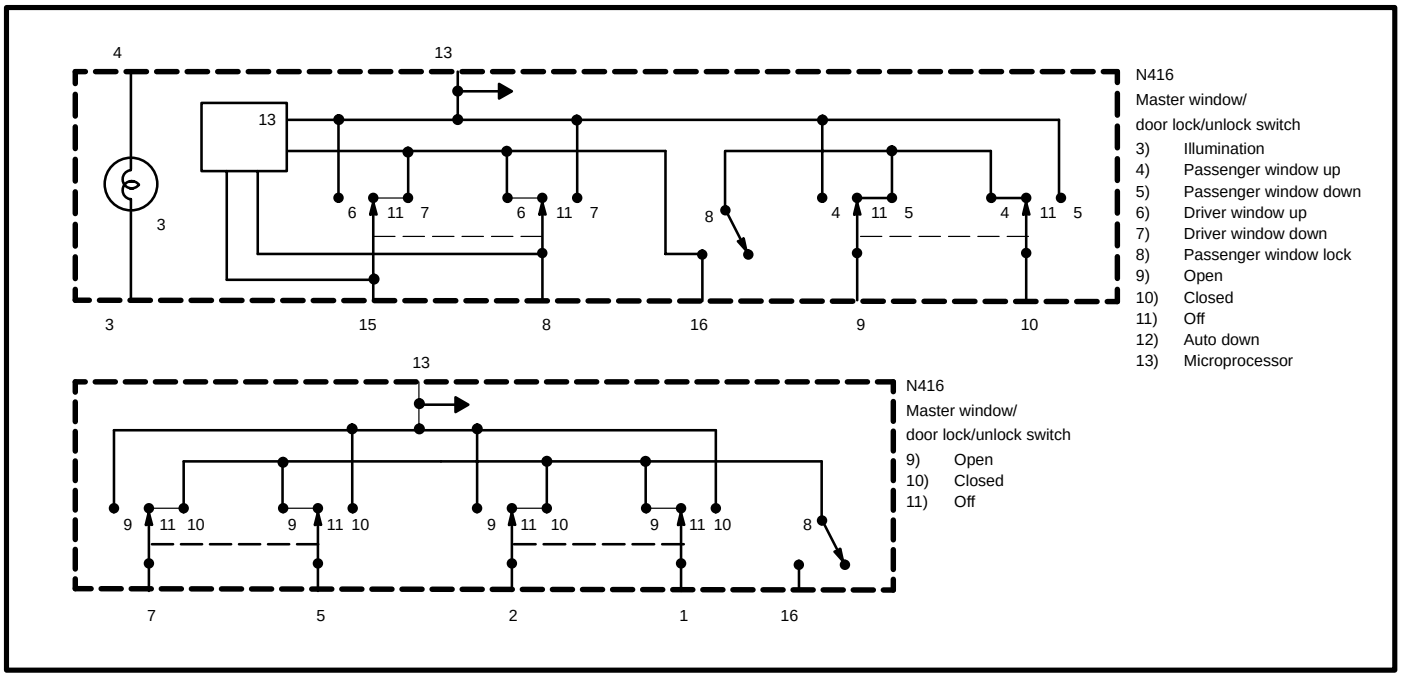
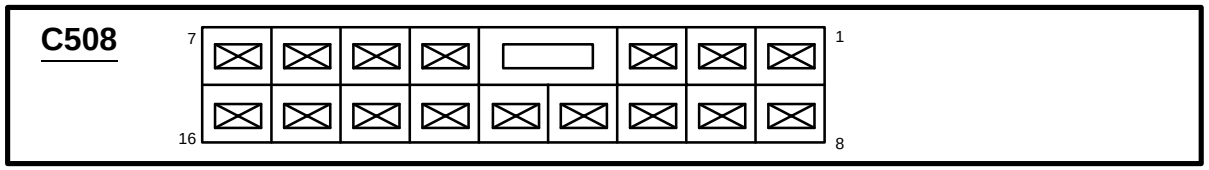
Terminal locations