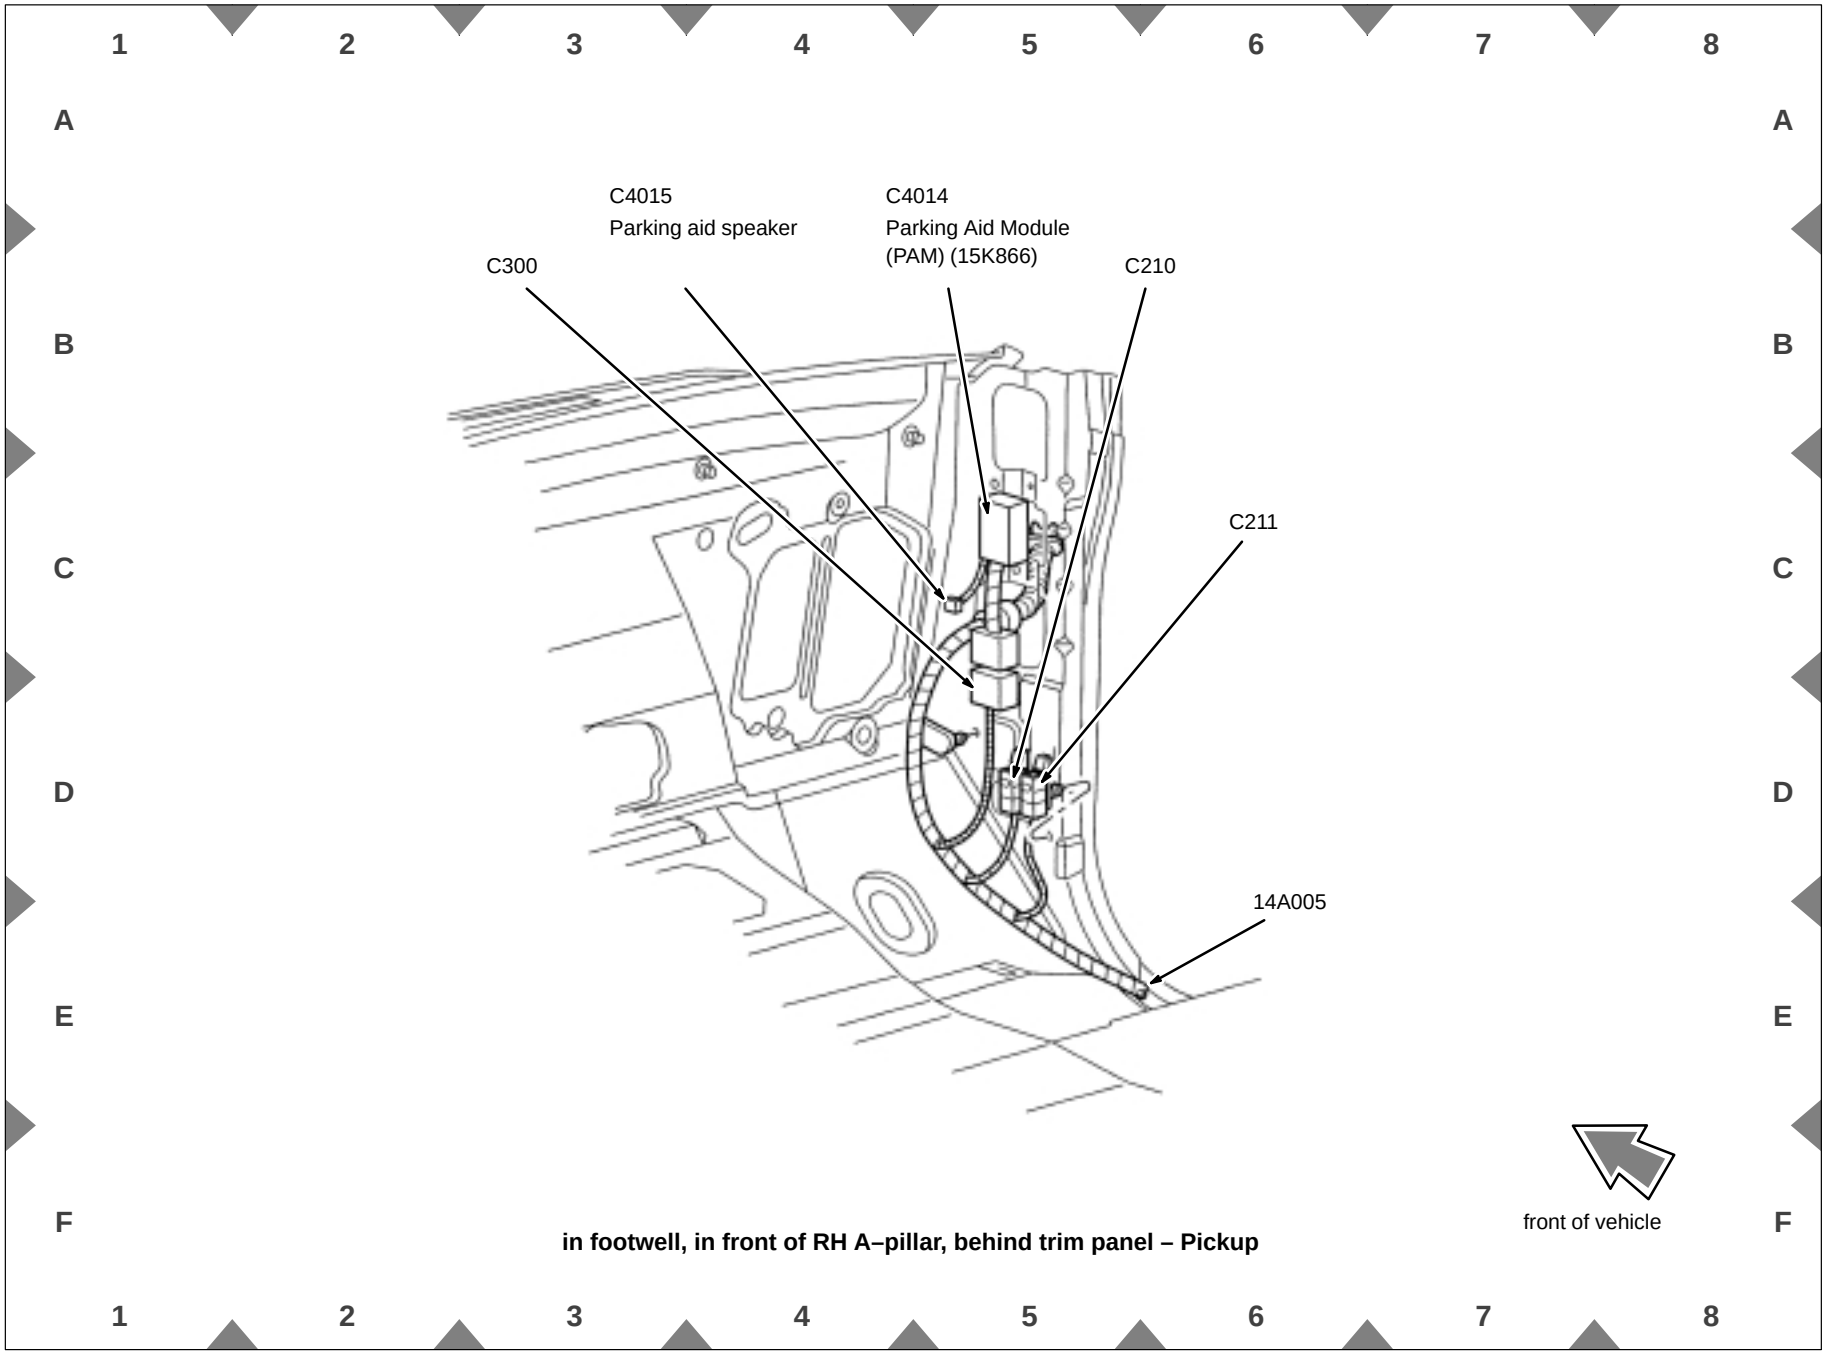

in footwell, in front of RH A–pillar, behind trim panel – Pickup