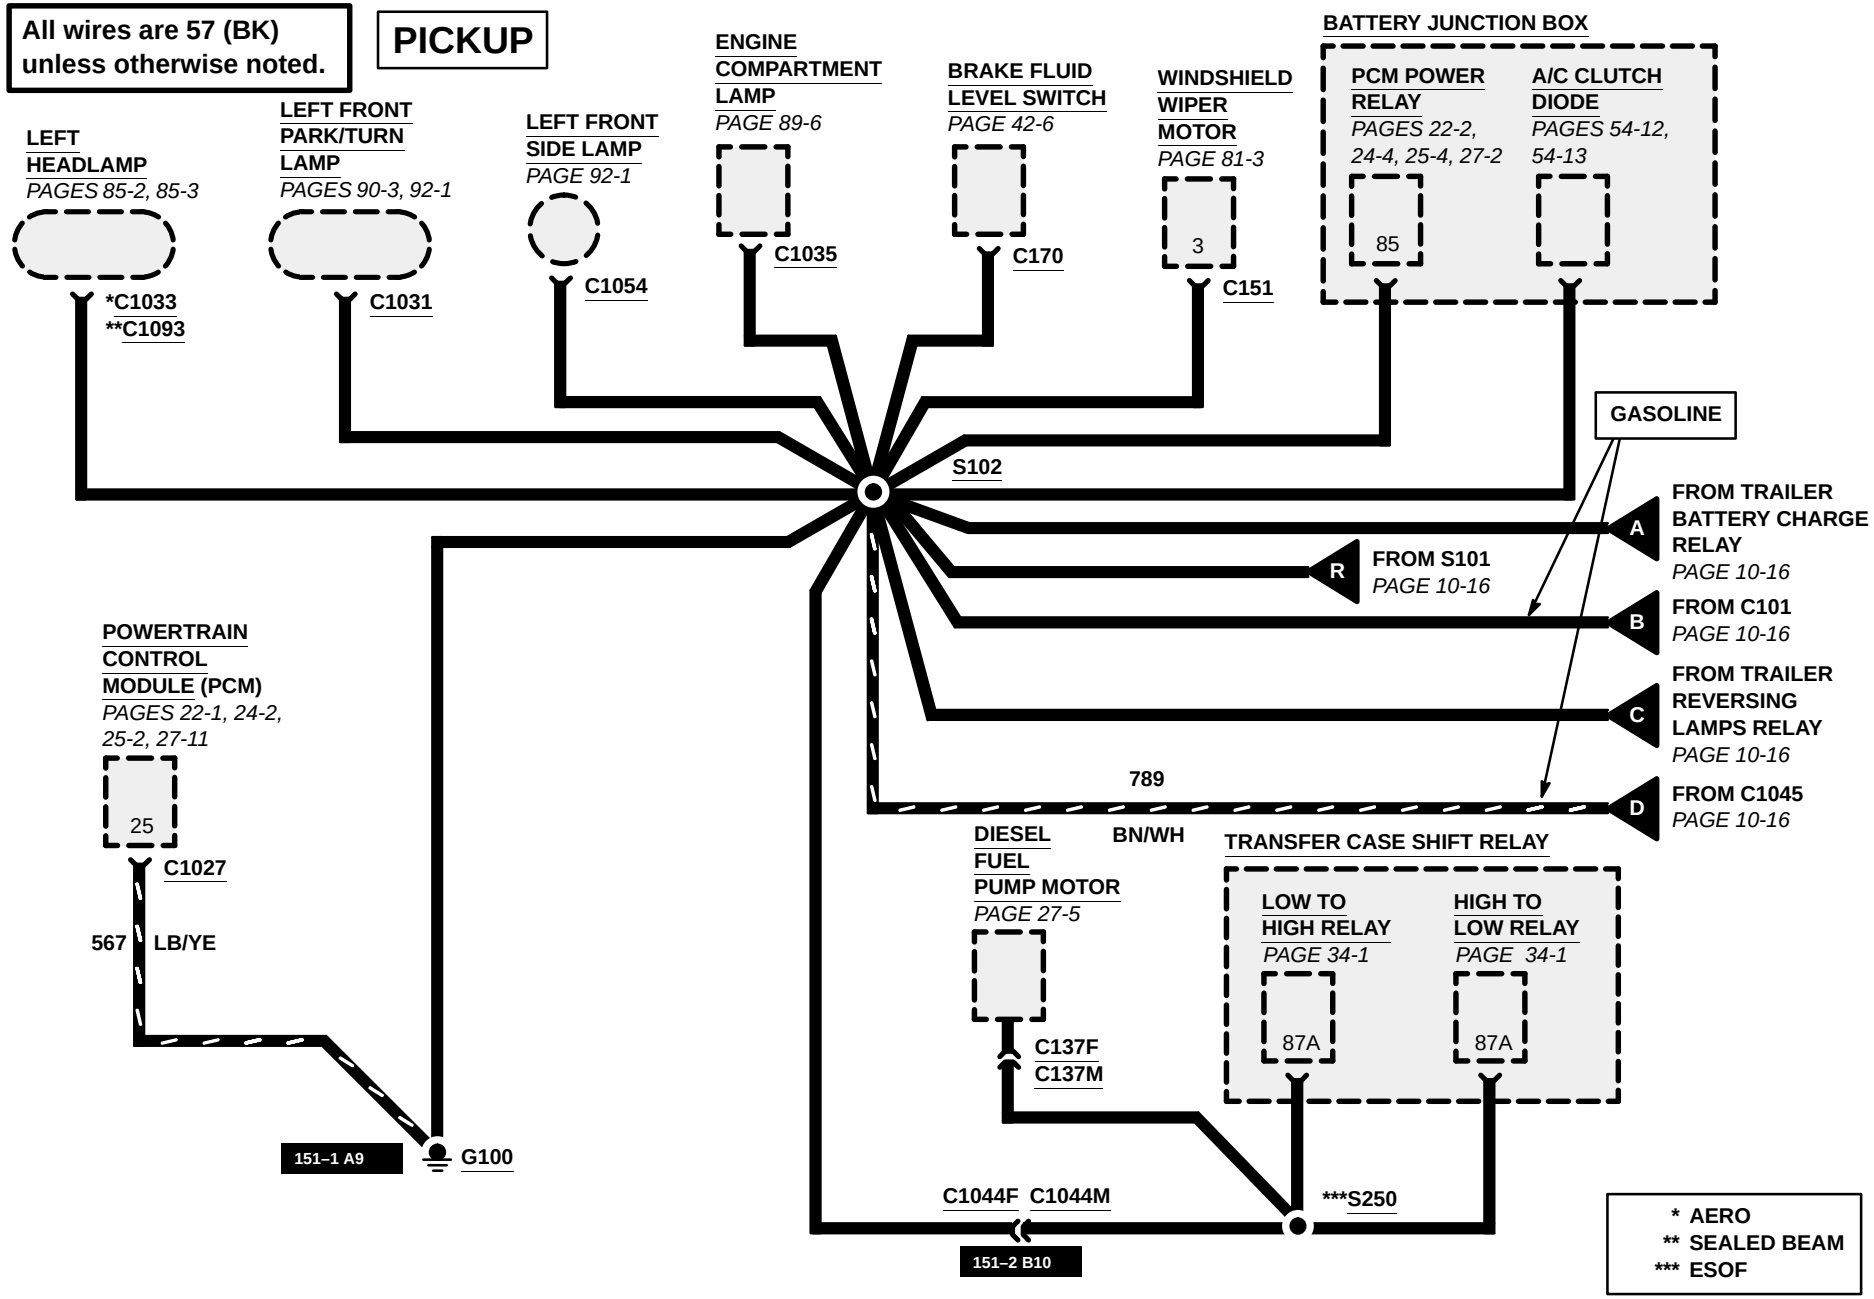10-15 GROUNDS