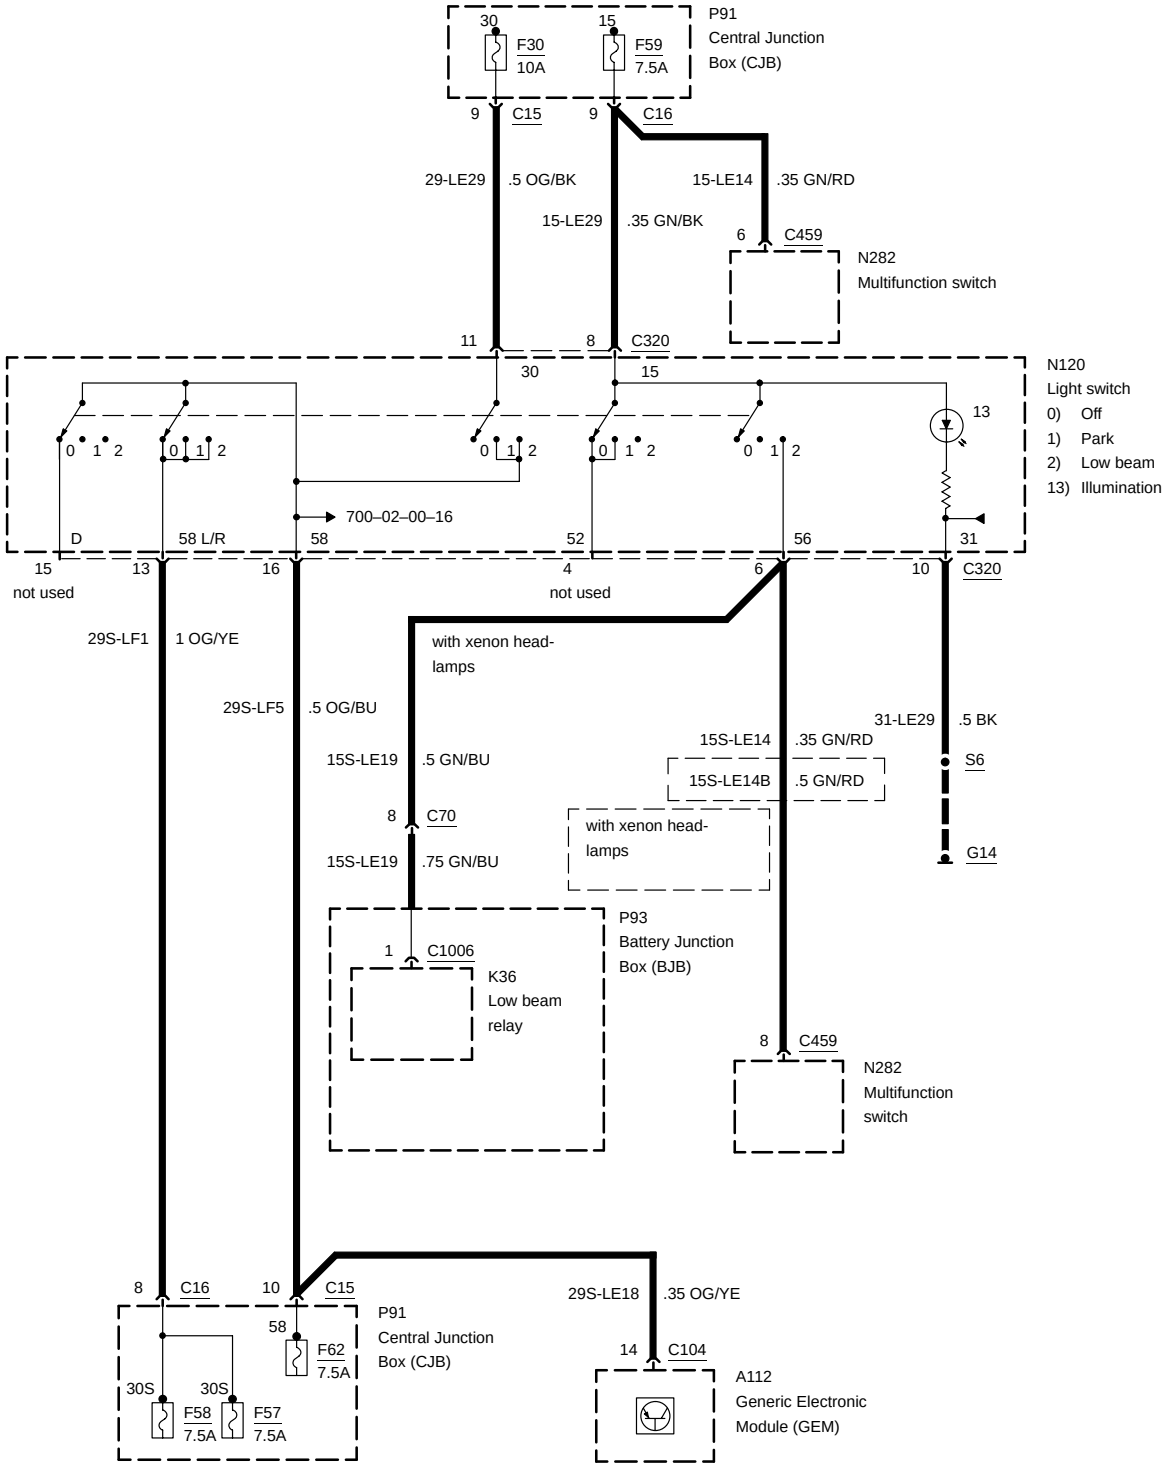Light switch, without daytime running lamps -14