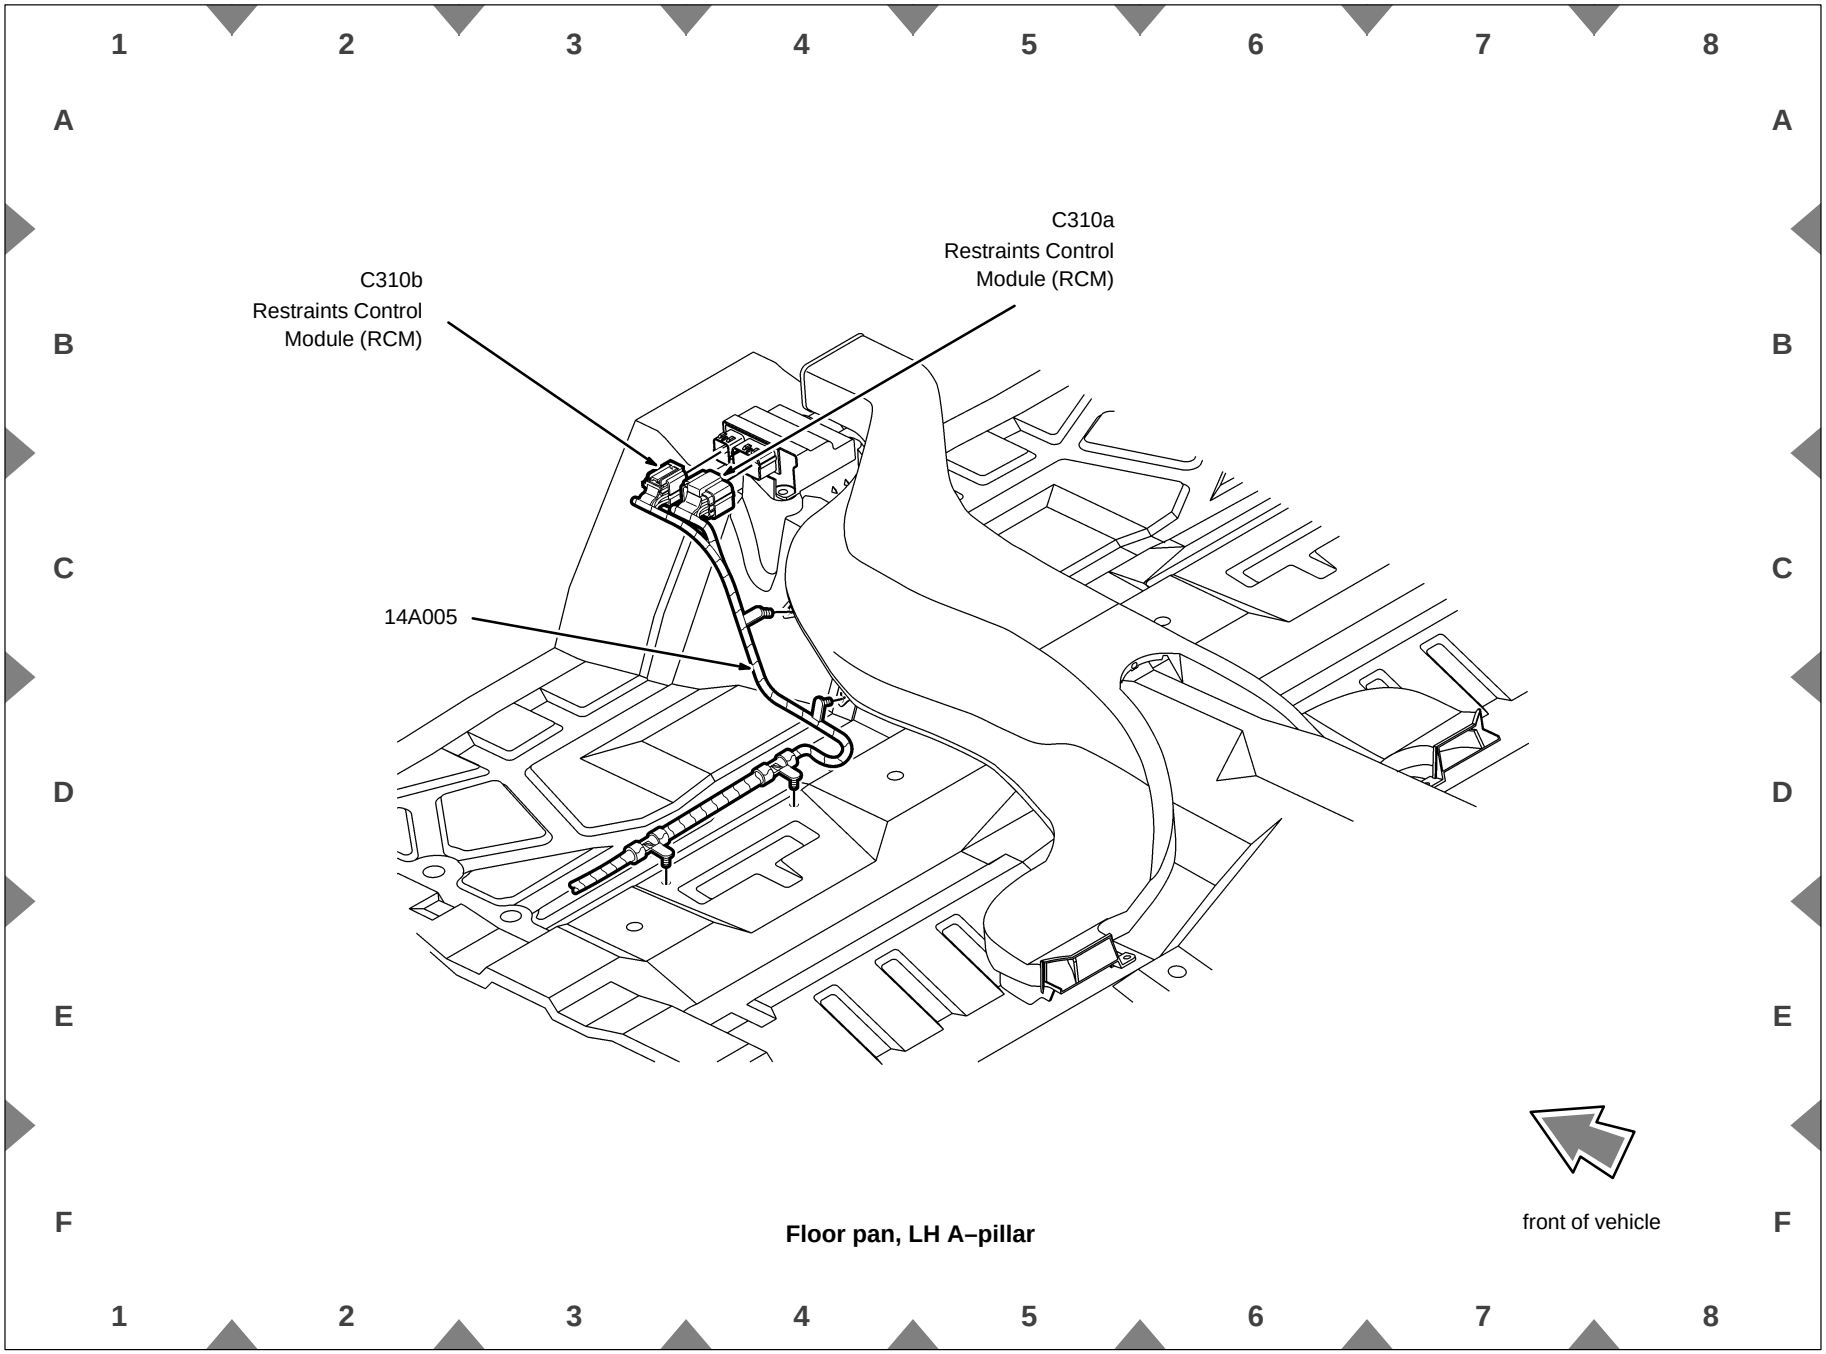


Floor pan, LH A–pillar