111-1 KEYLESS ENTRY (ILLUMINATED ENTRY)
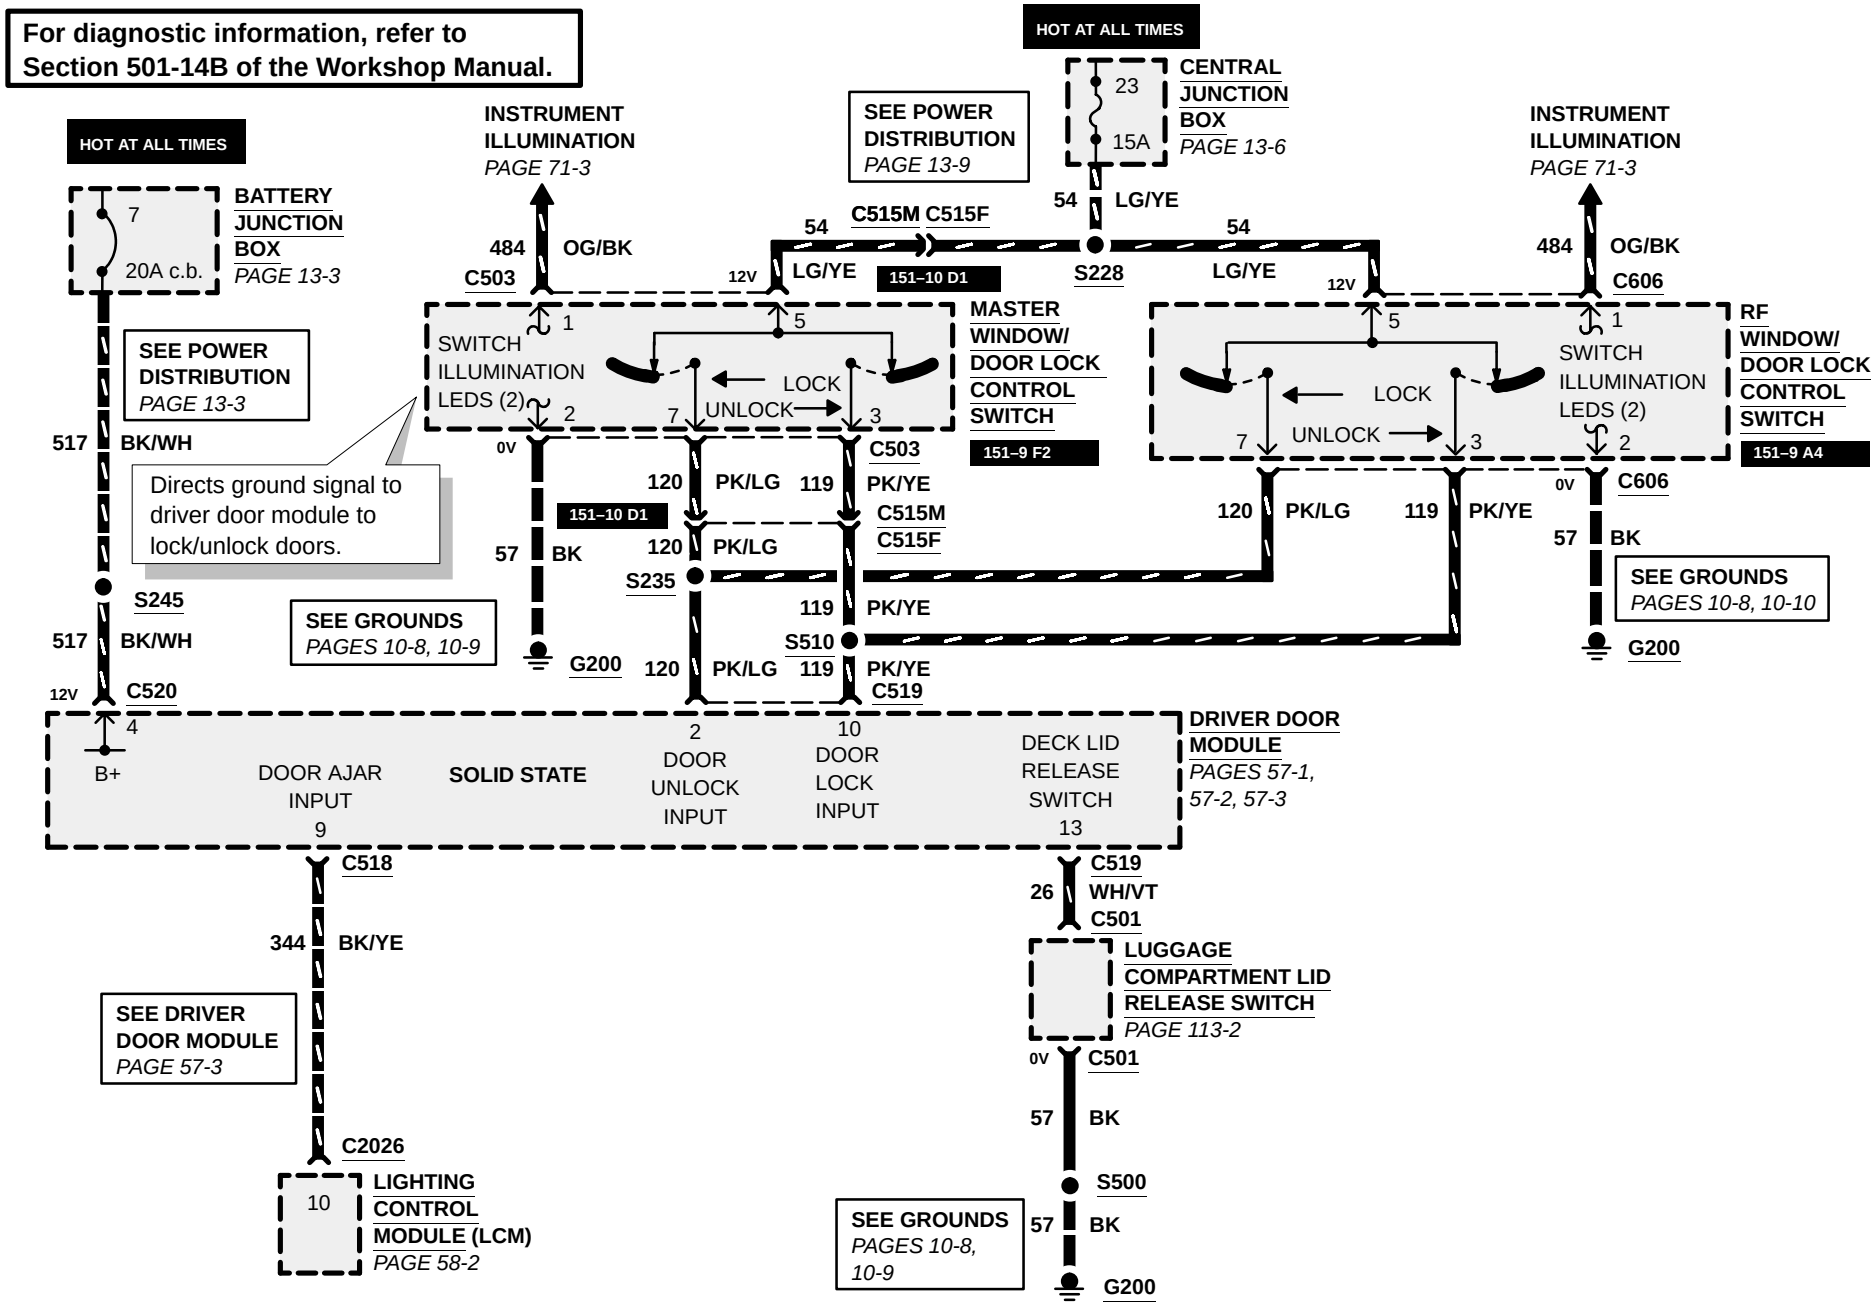
2001 CROWN VICTORIA/GRAND MARQUIS