151-5 COMPONENT LOCATION VIEWS

2001 CONTINENTAL

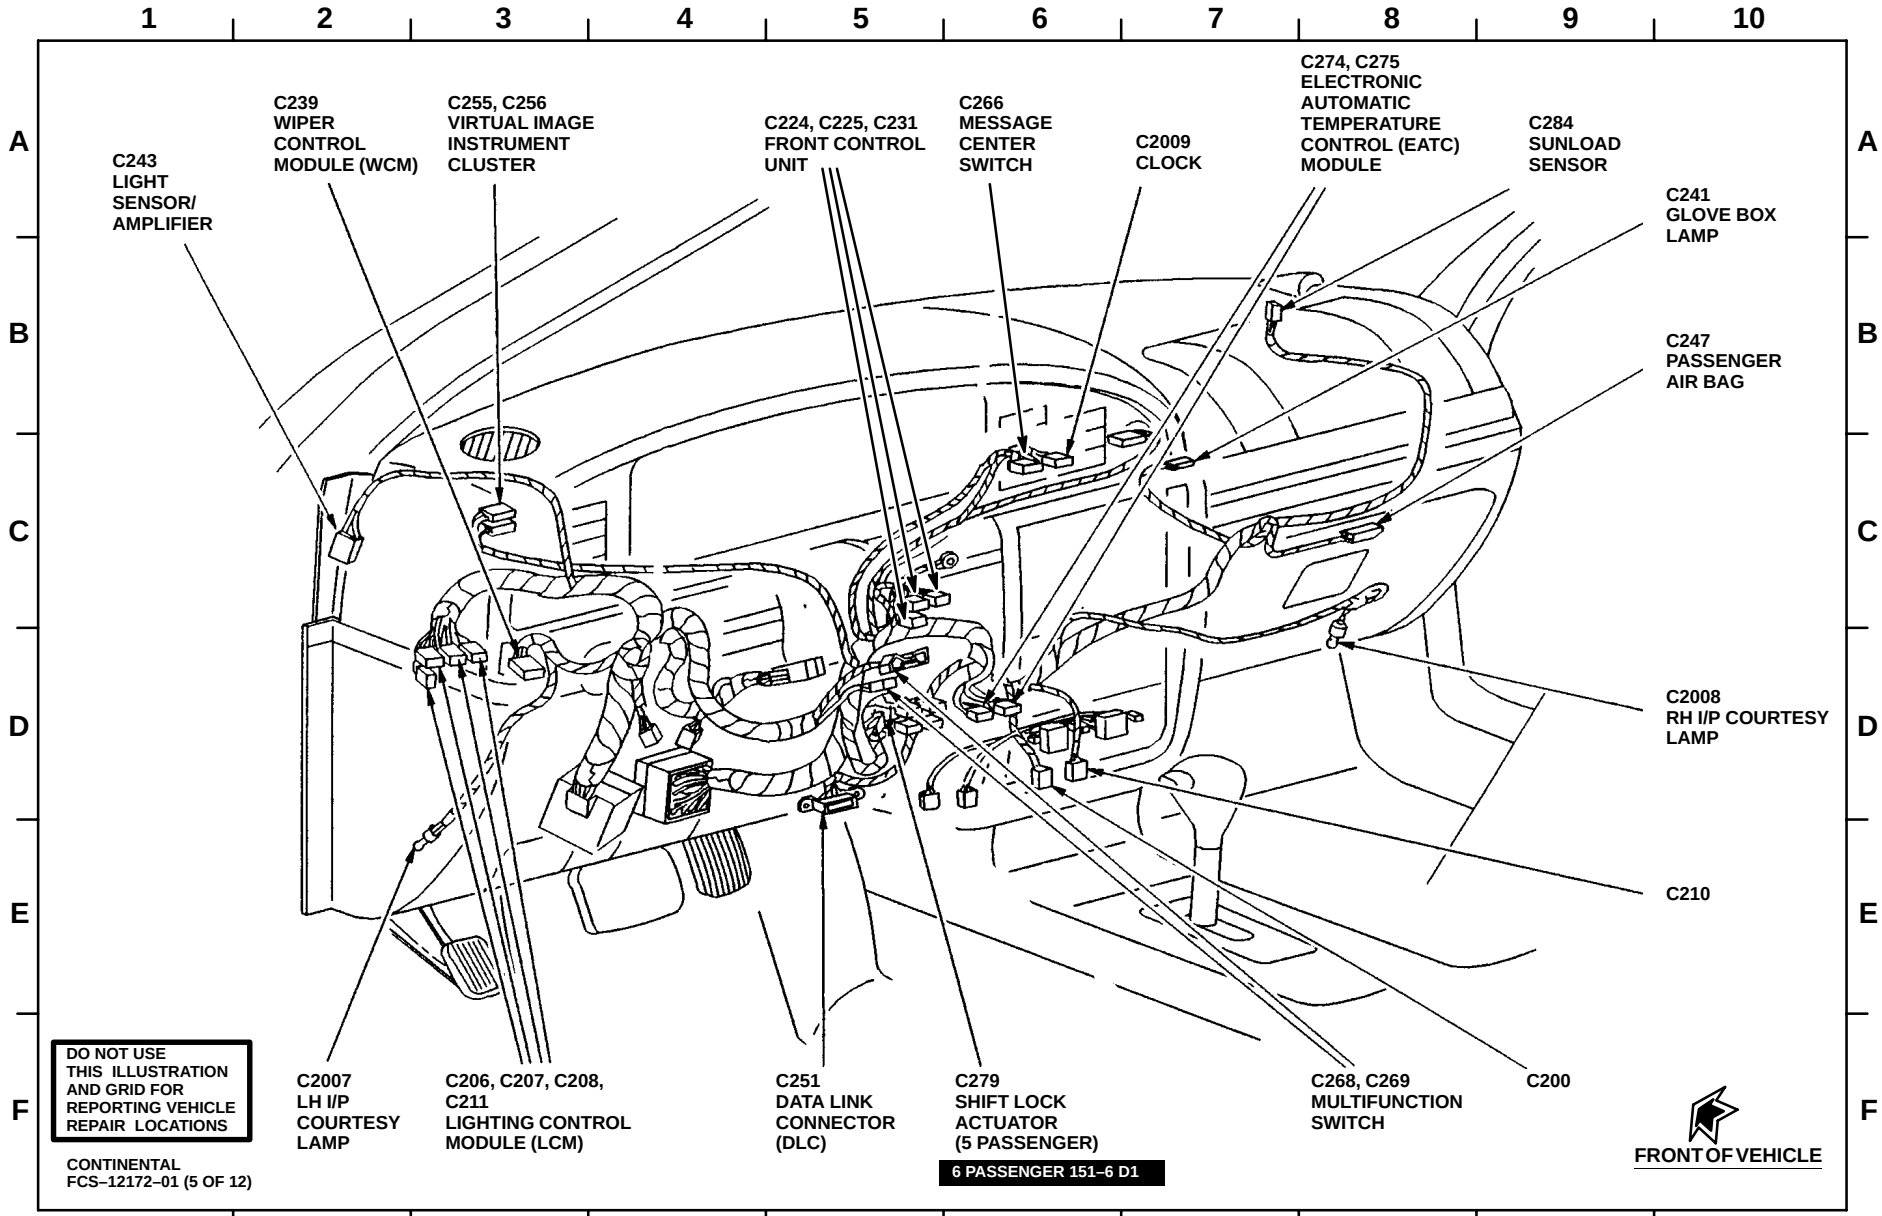

BEHIND I/P (1 OF 2)