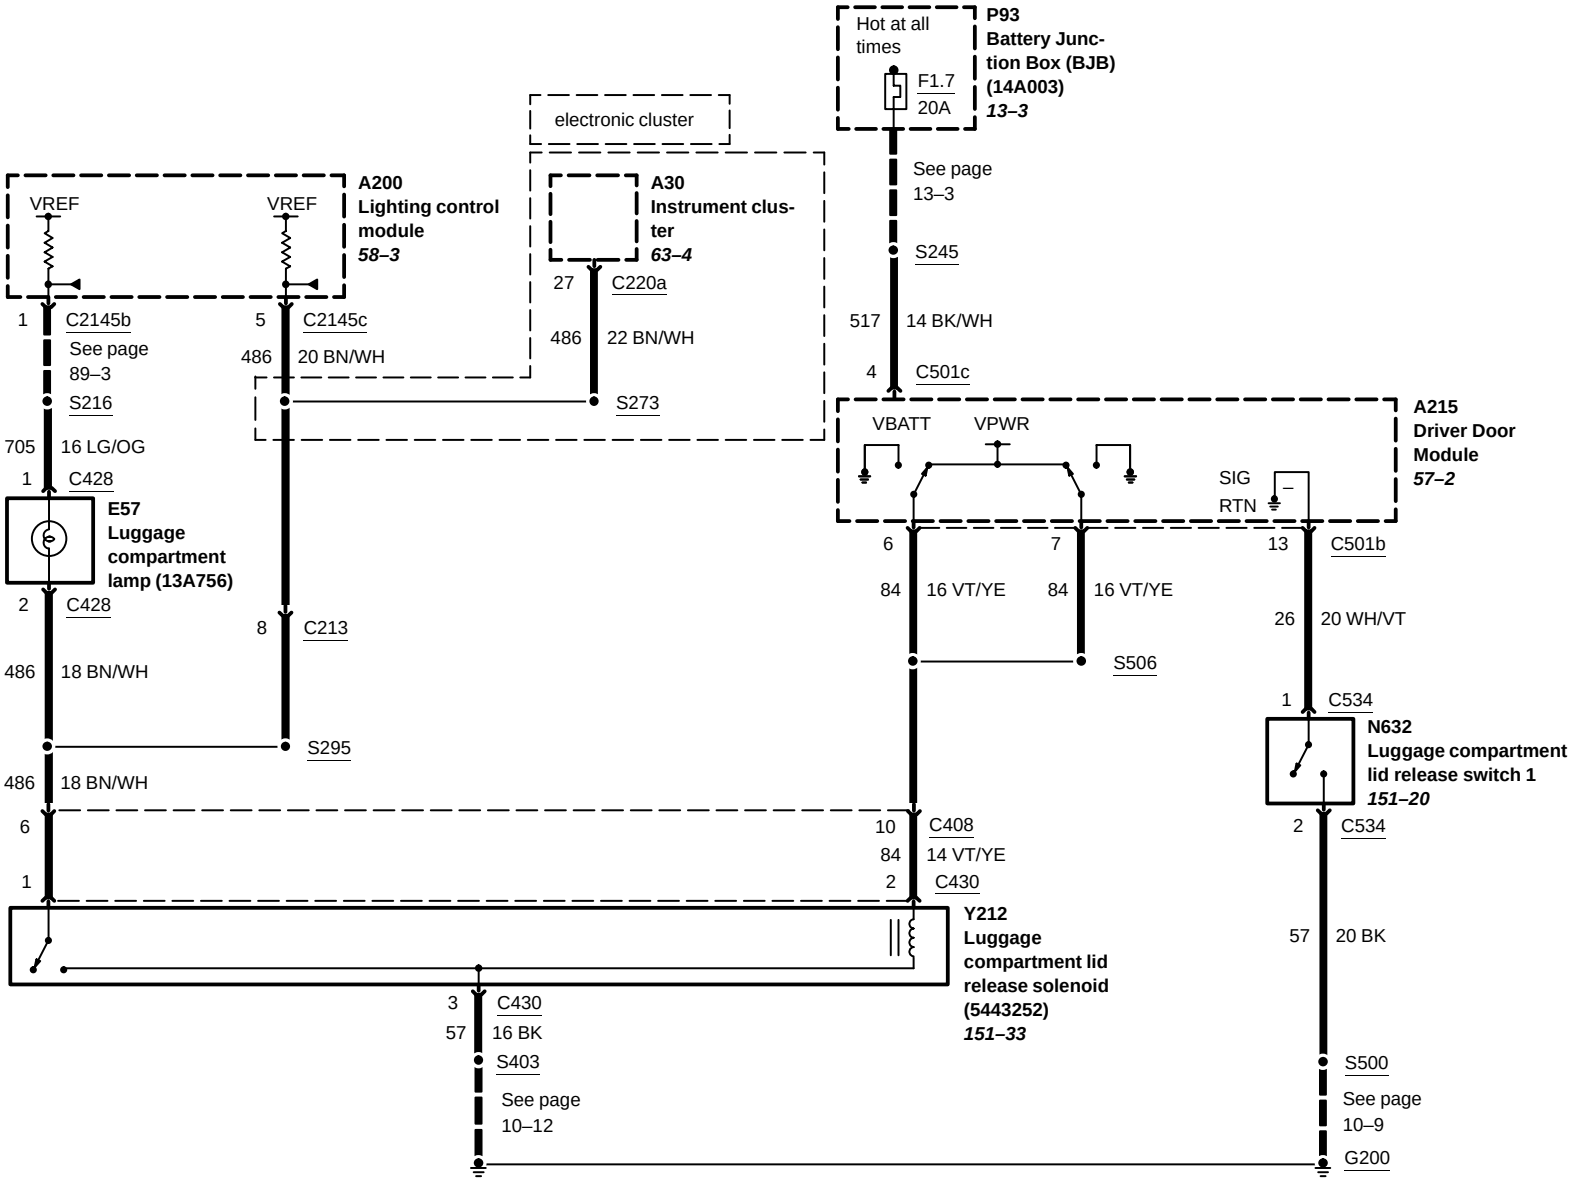with keyless entry