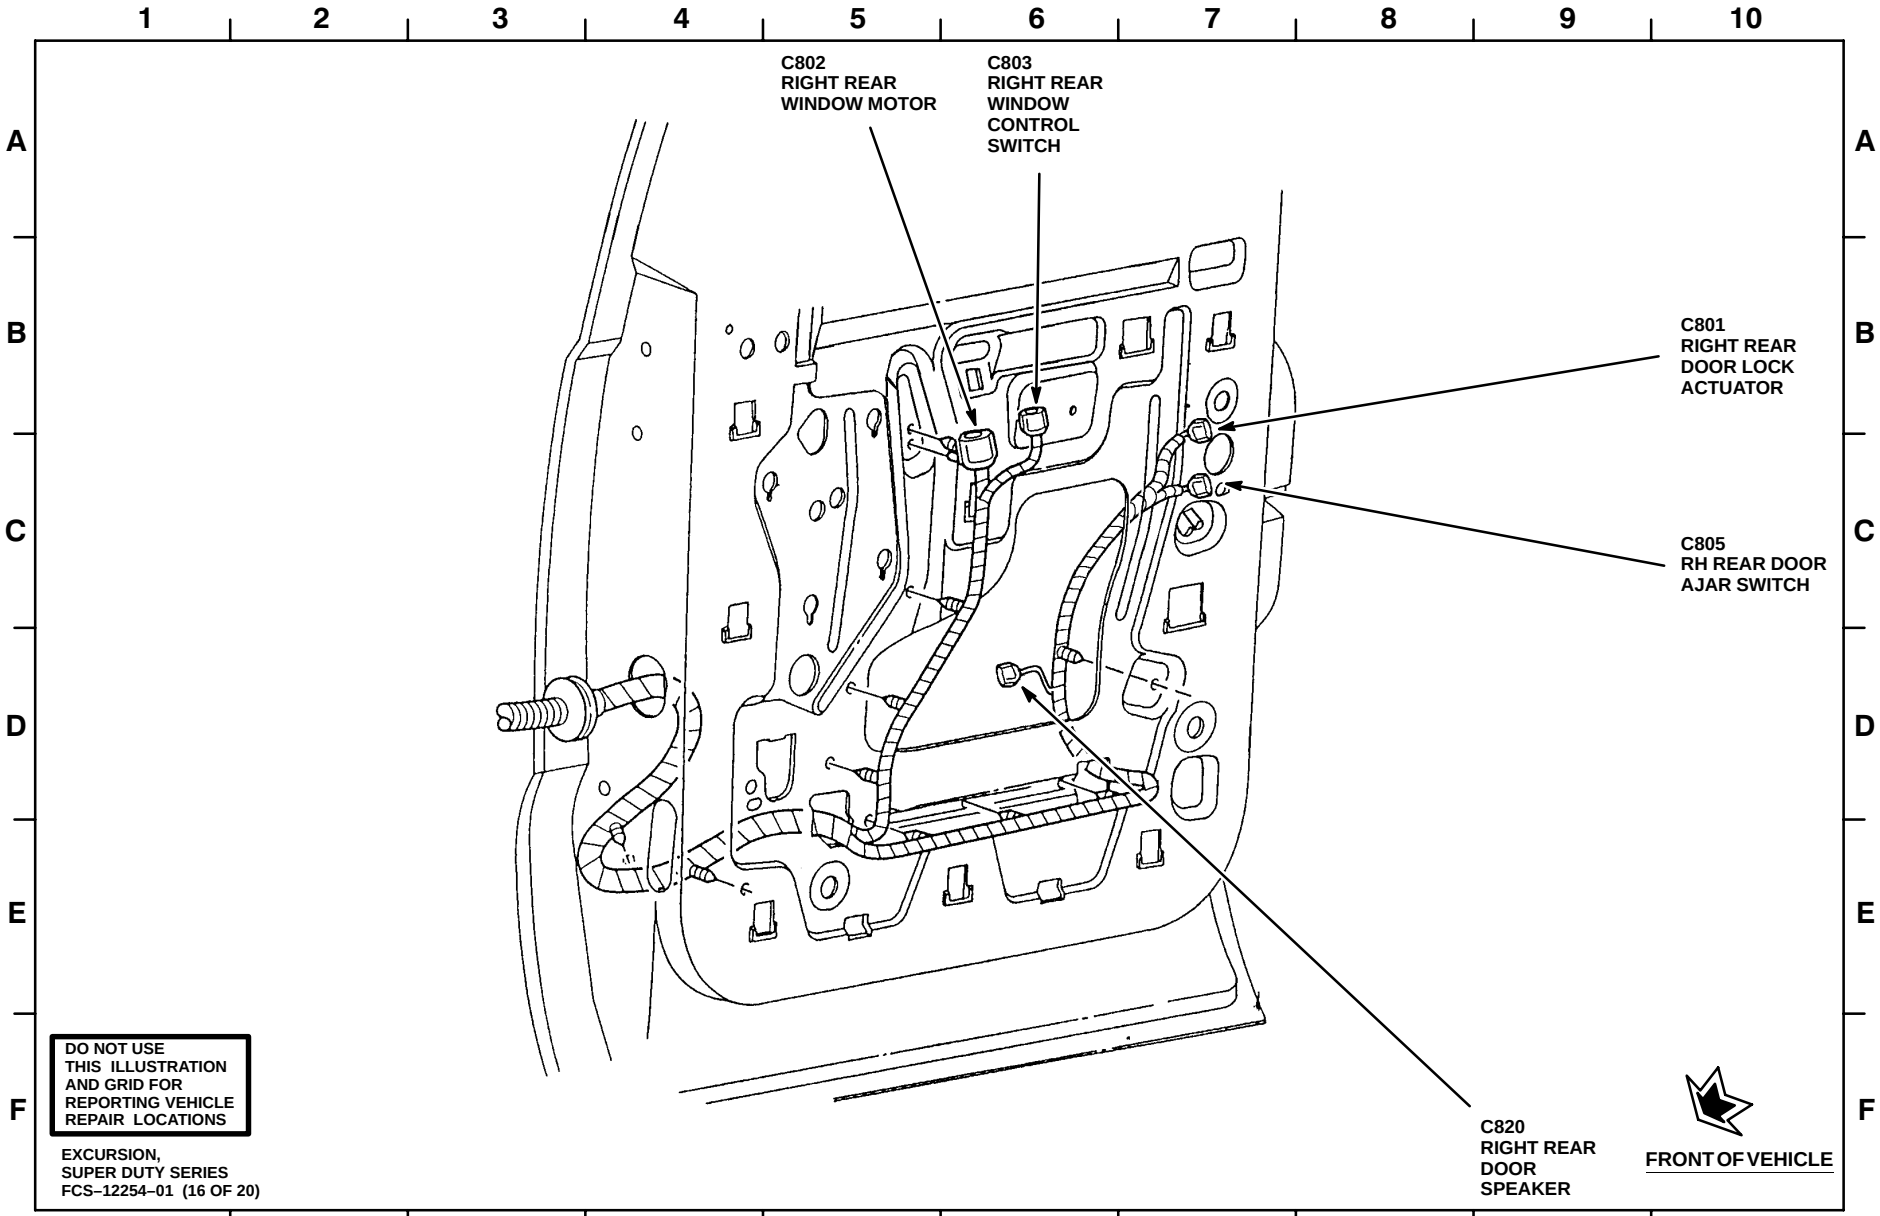

RIGHT REAR DOOR (EXCURSION)