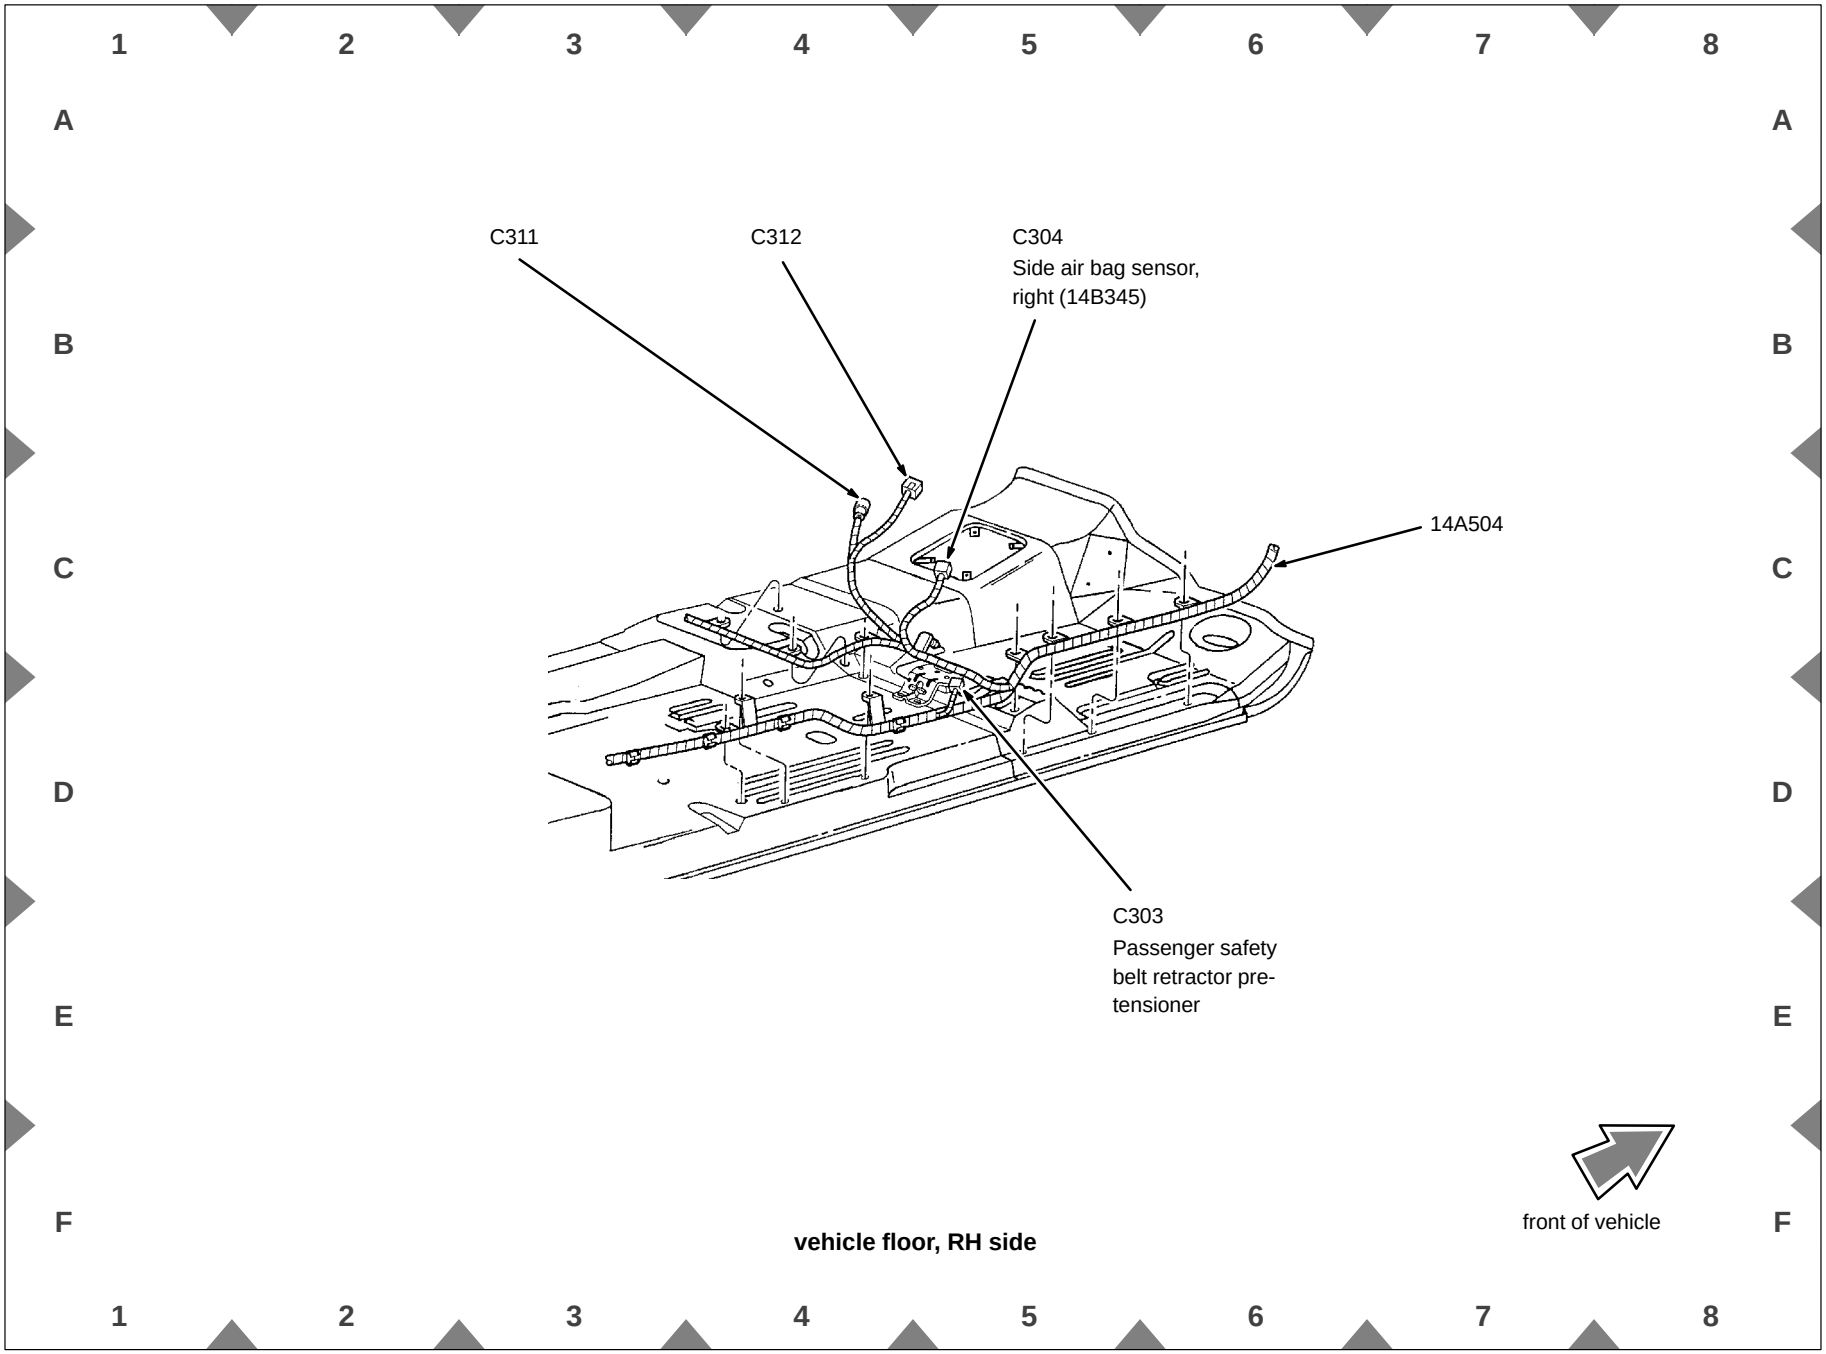

vehicle floor, RH side