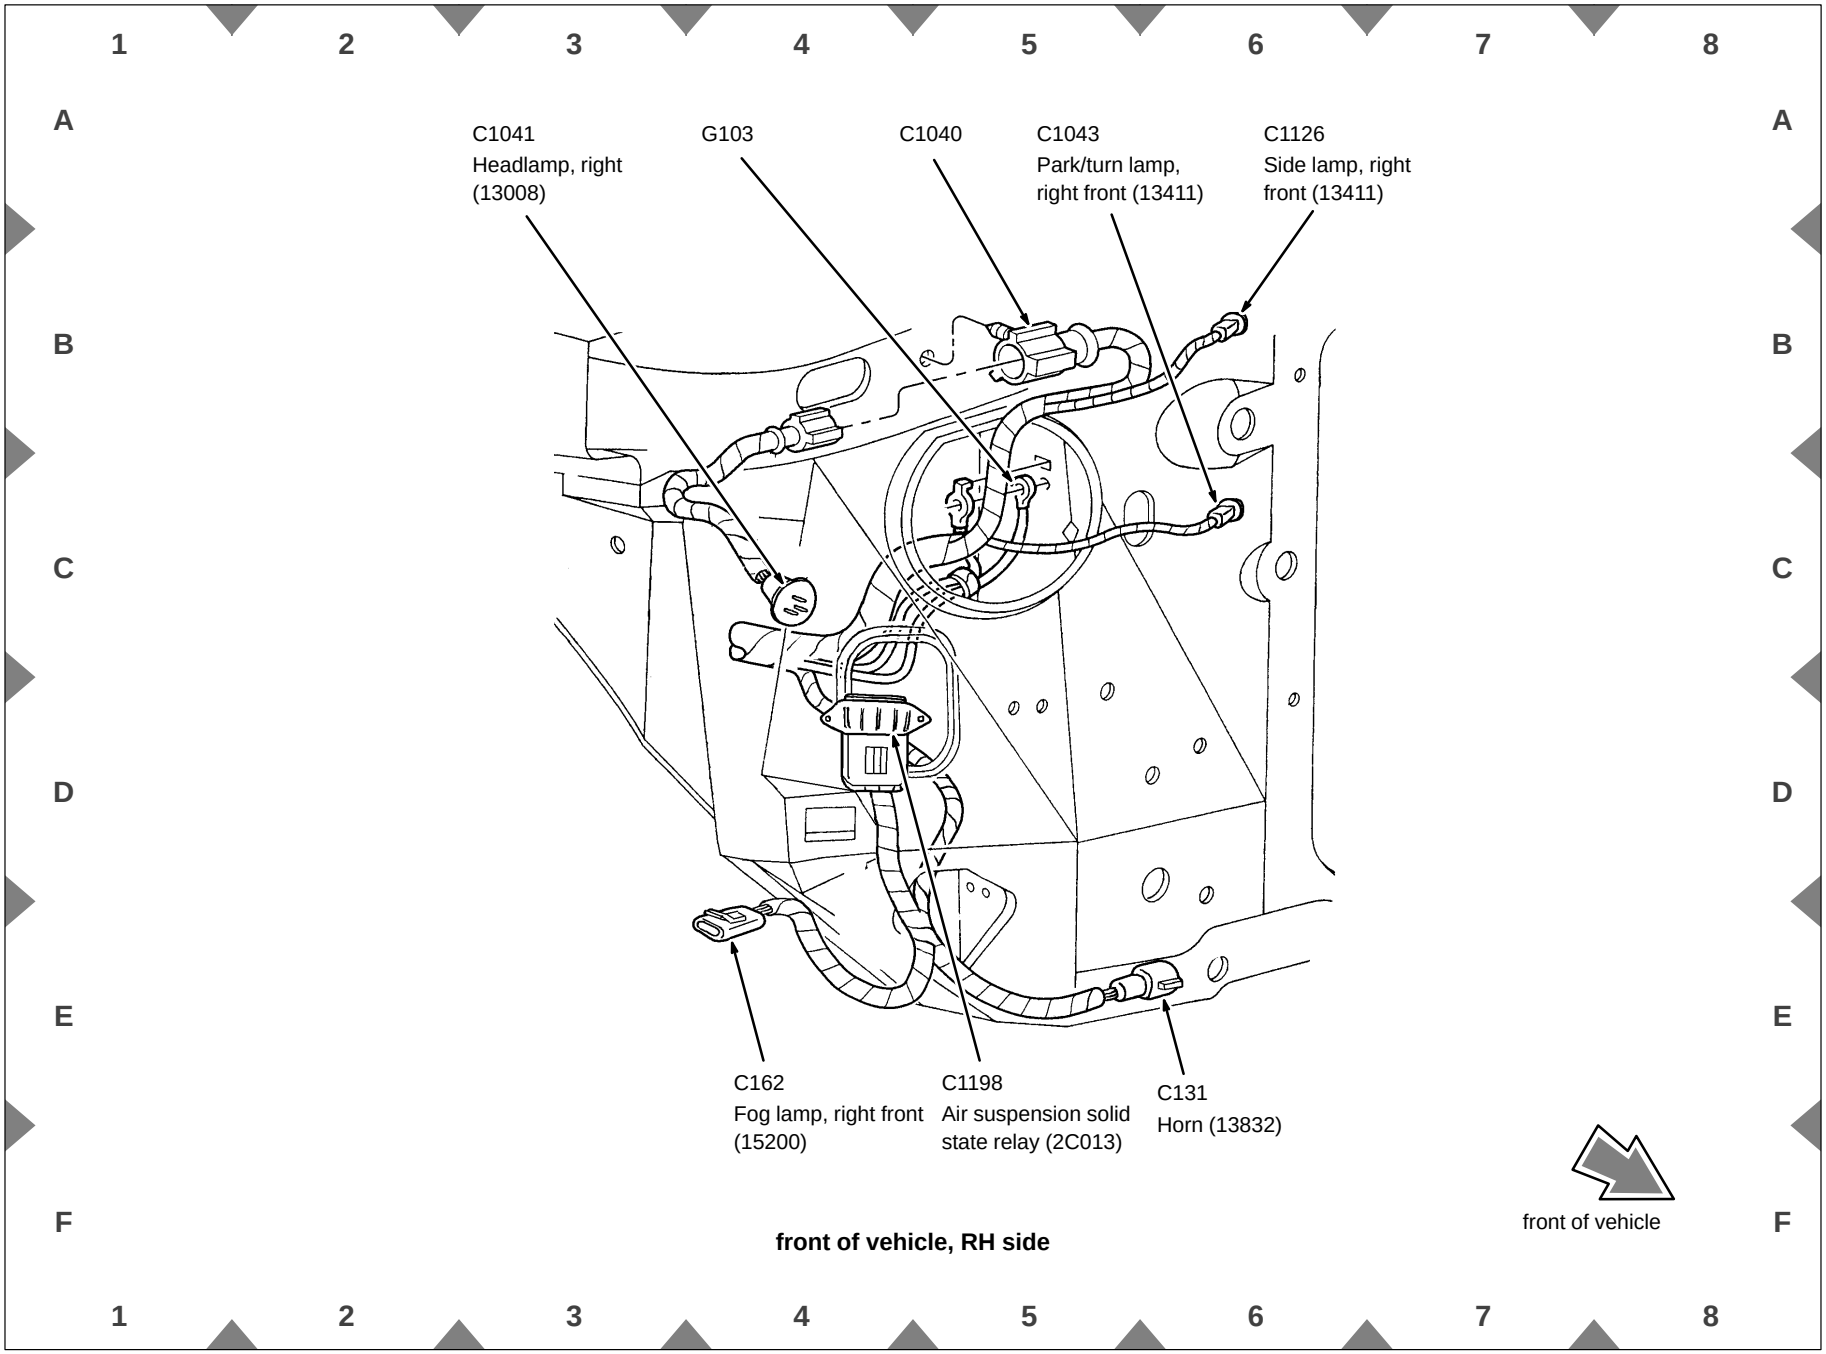


**front of vehicle, RH side**