REVISED
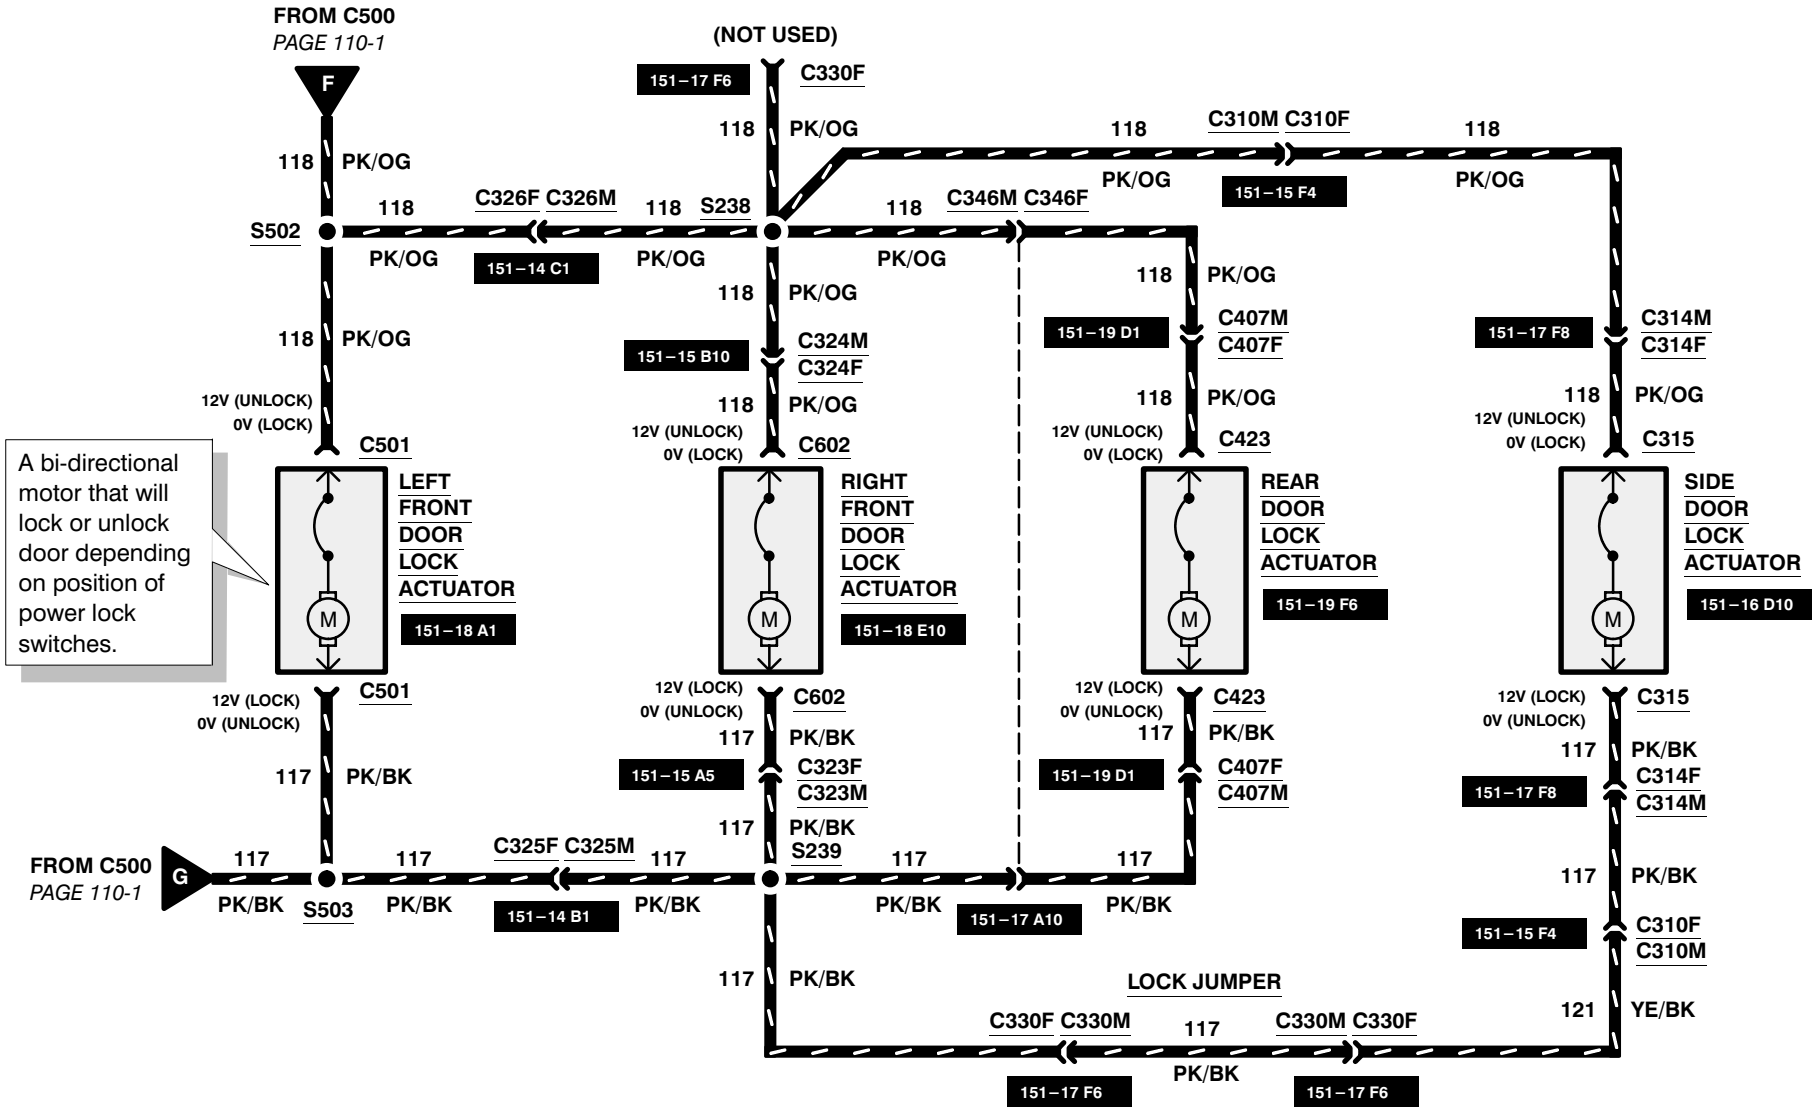
W/HINGED DOOR