TERMINALS

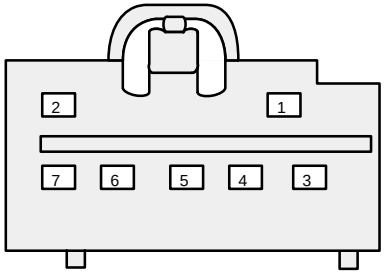

C509

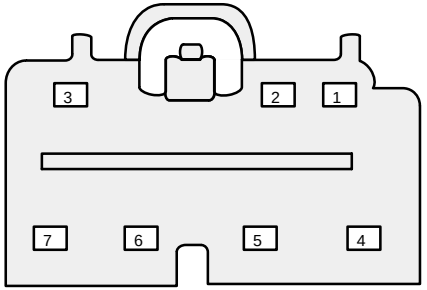

C510
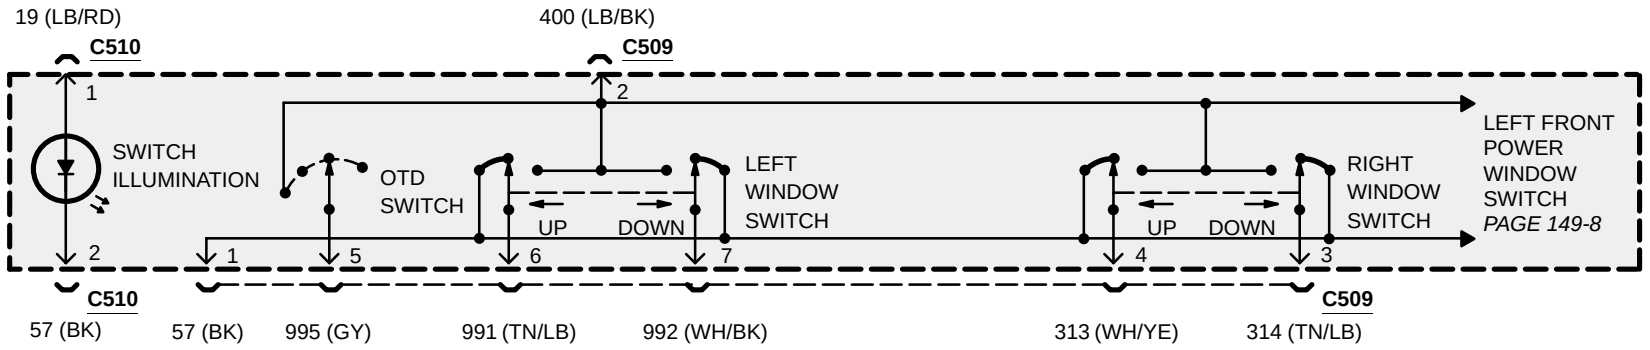
SCHEMATIC