111-1 KEYLESS ENTRY
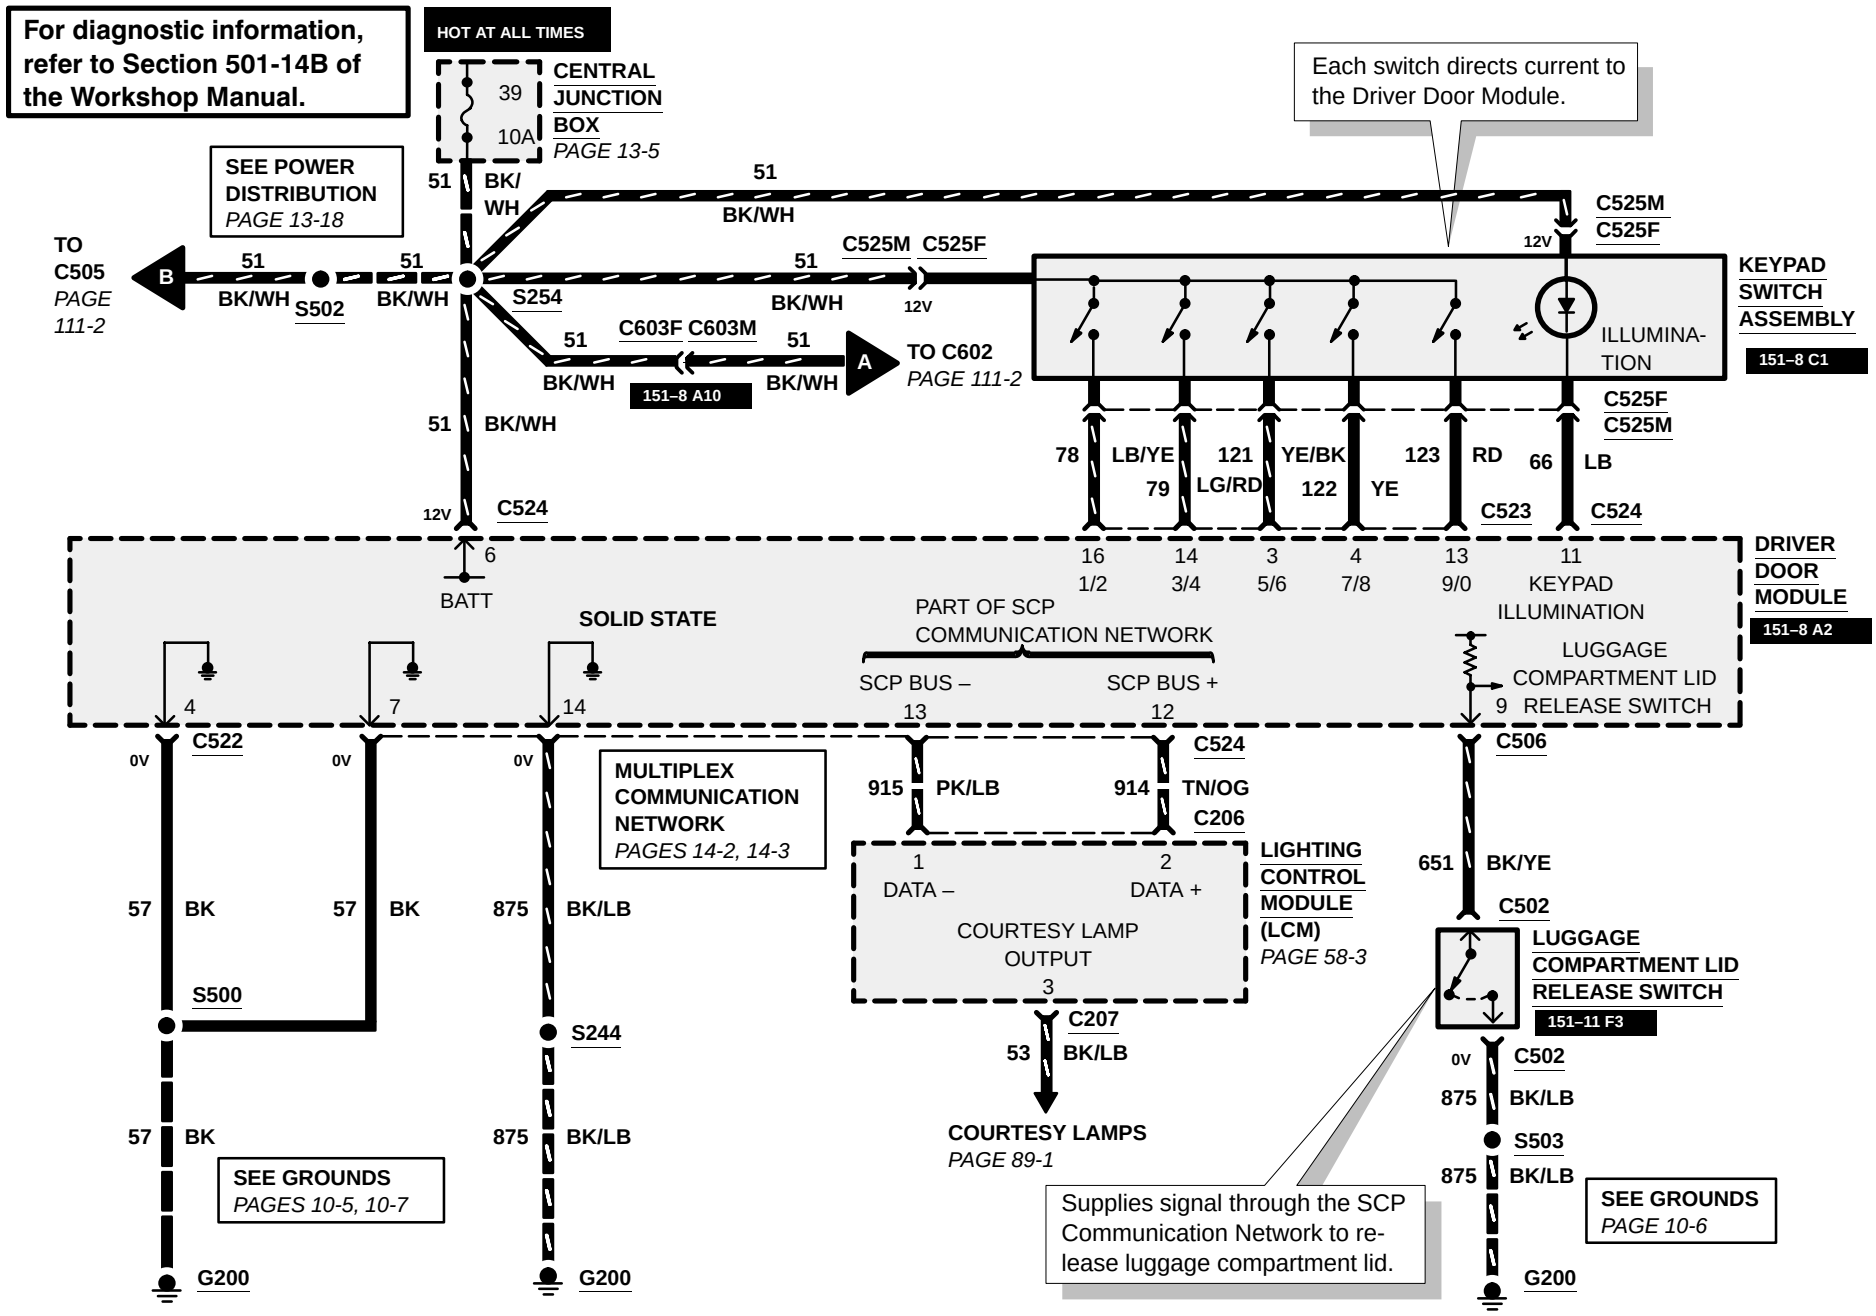
2001 CONTINENTAL