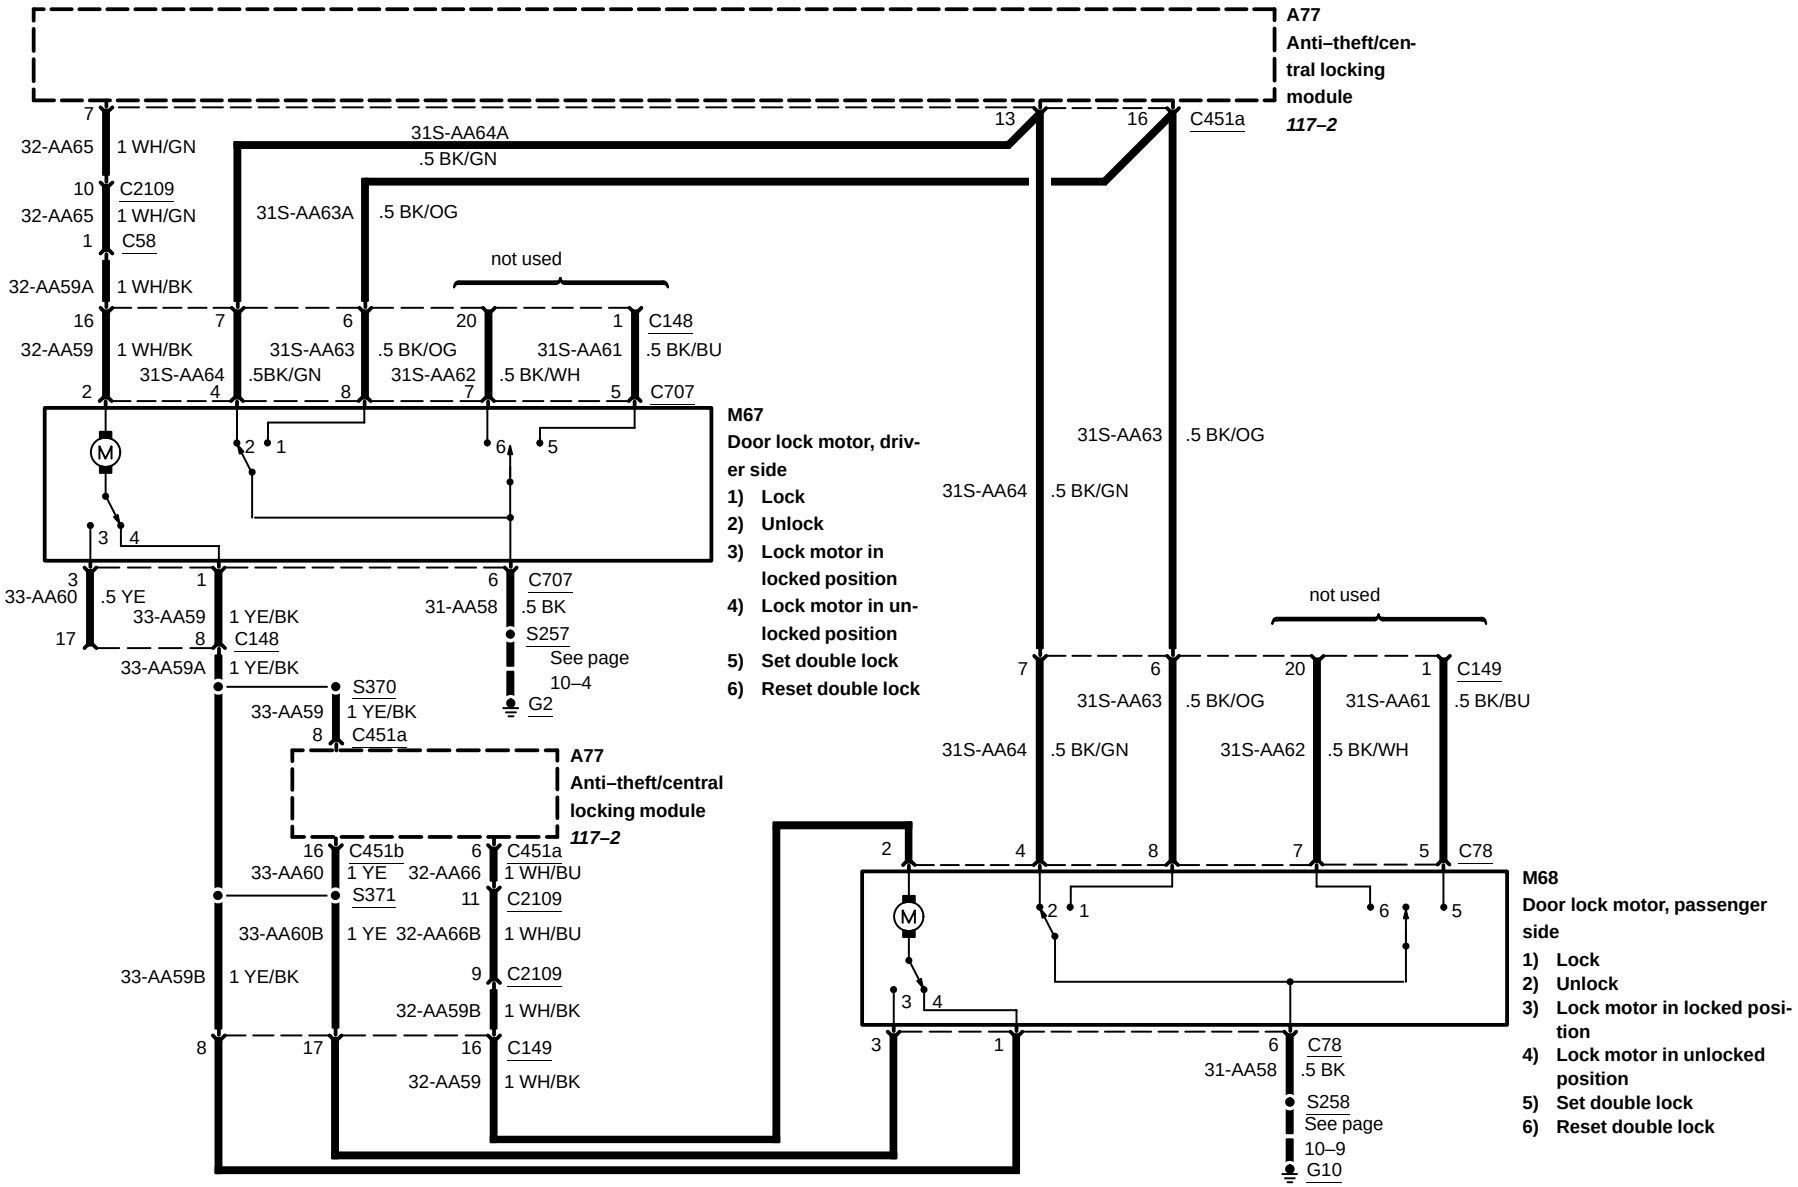## without remote keyless entry