10-1 GROUNDS

2001 TOWN CAR

All Circuits are 57 BK unless otherwise noted.

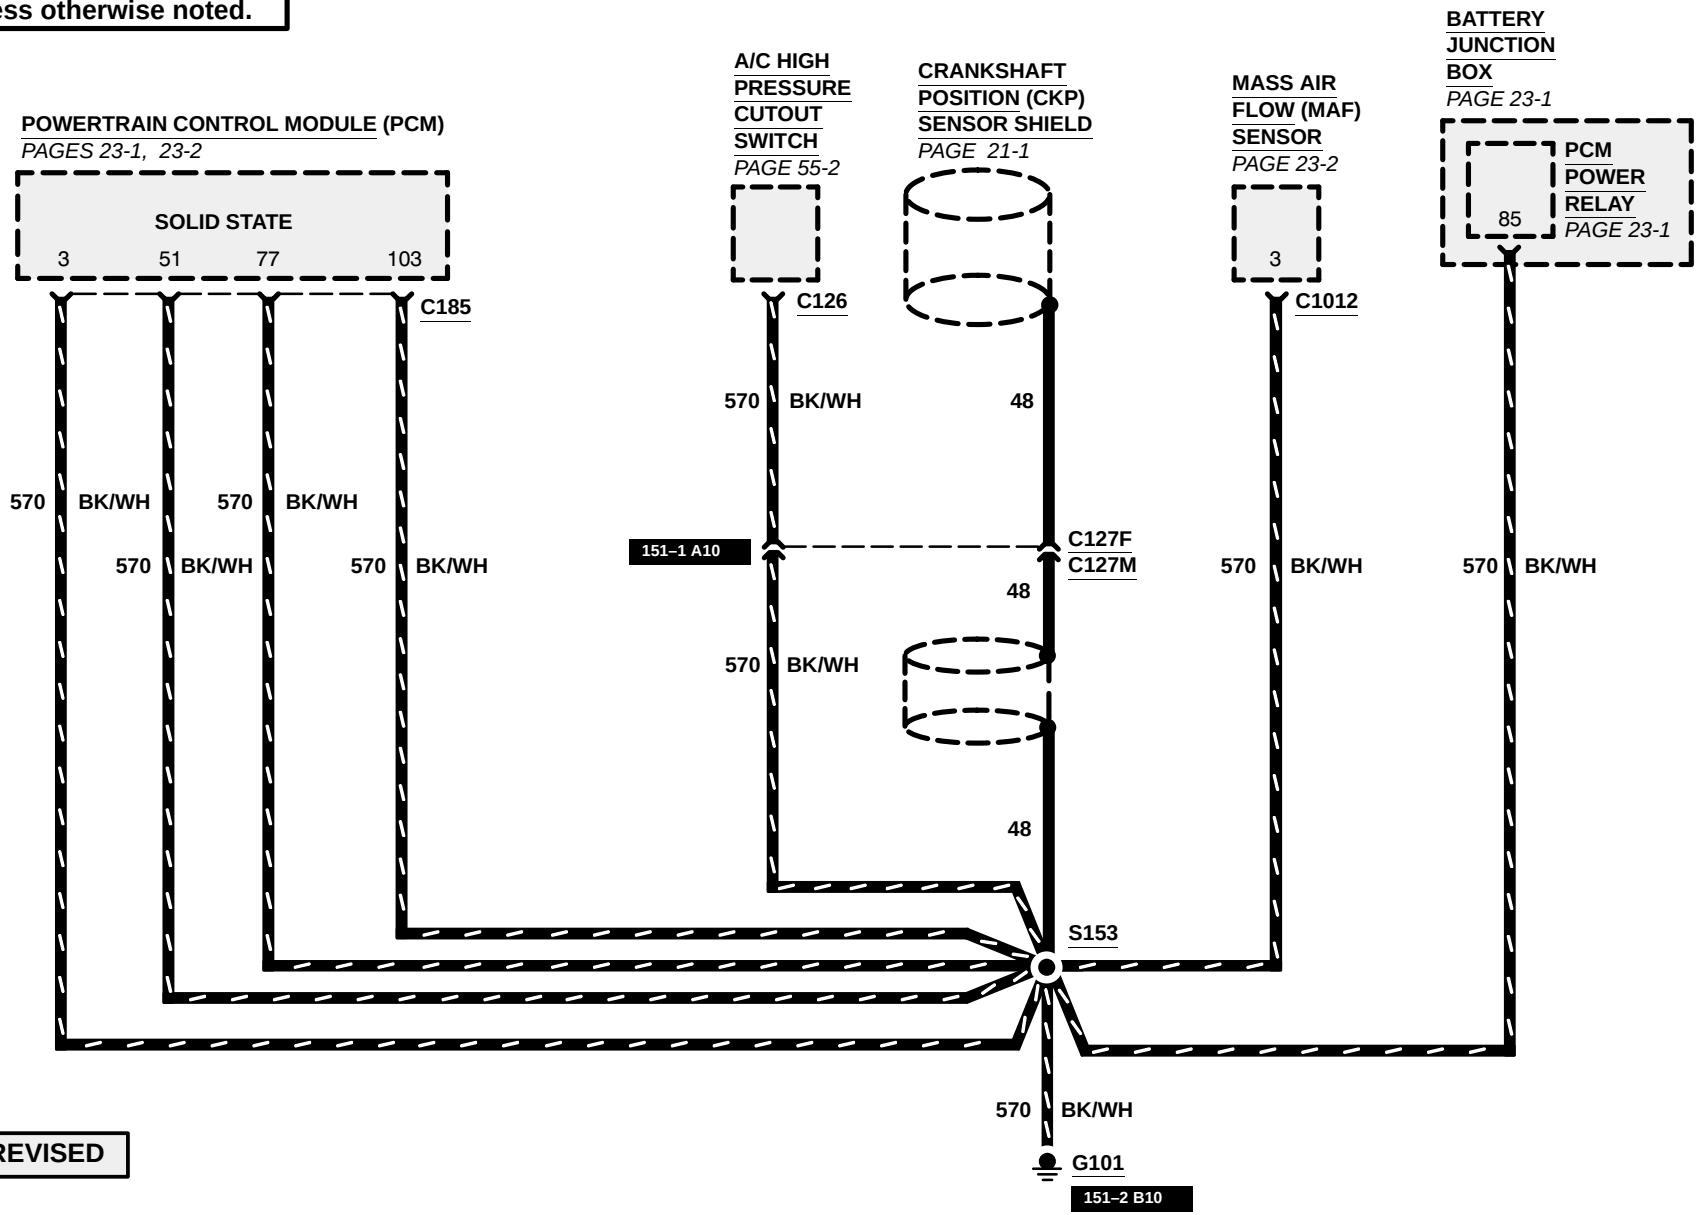

REVISED