13-29 POWER DISTRIBUTION
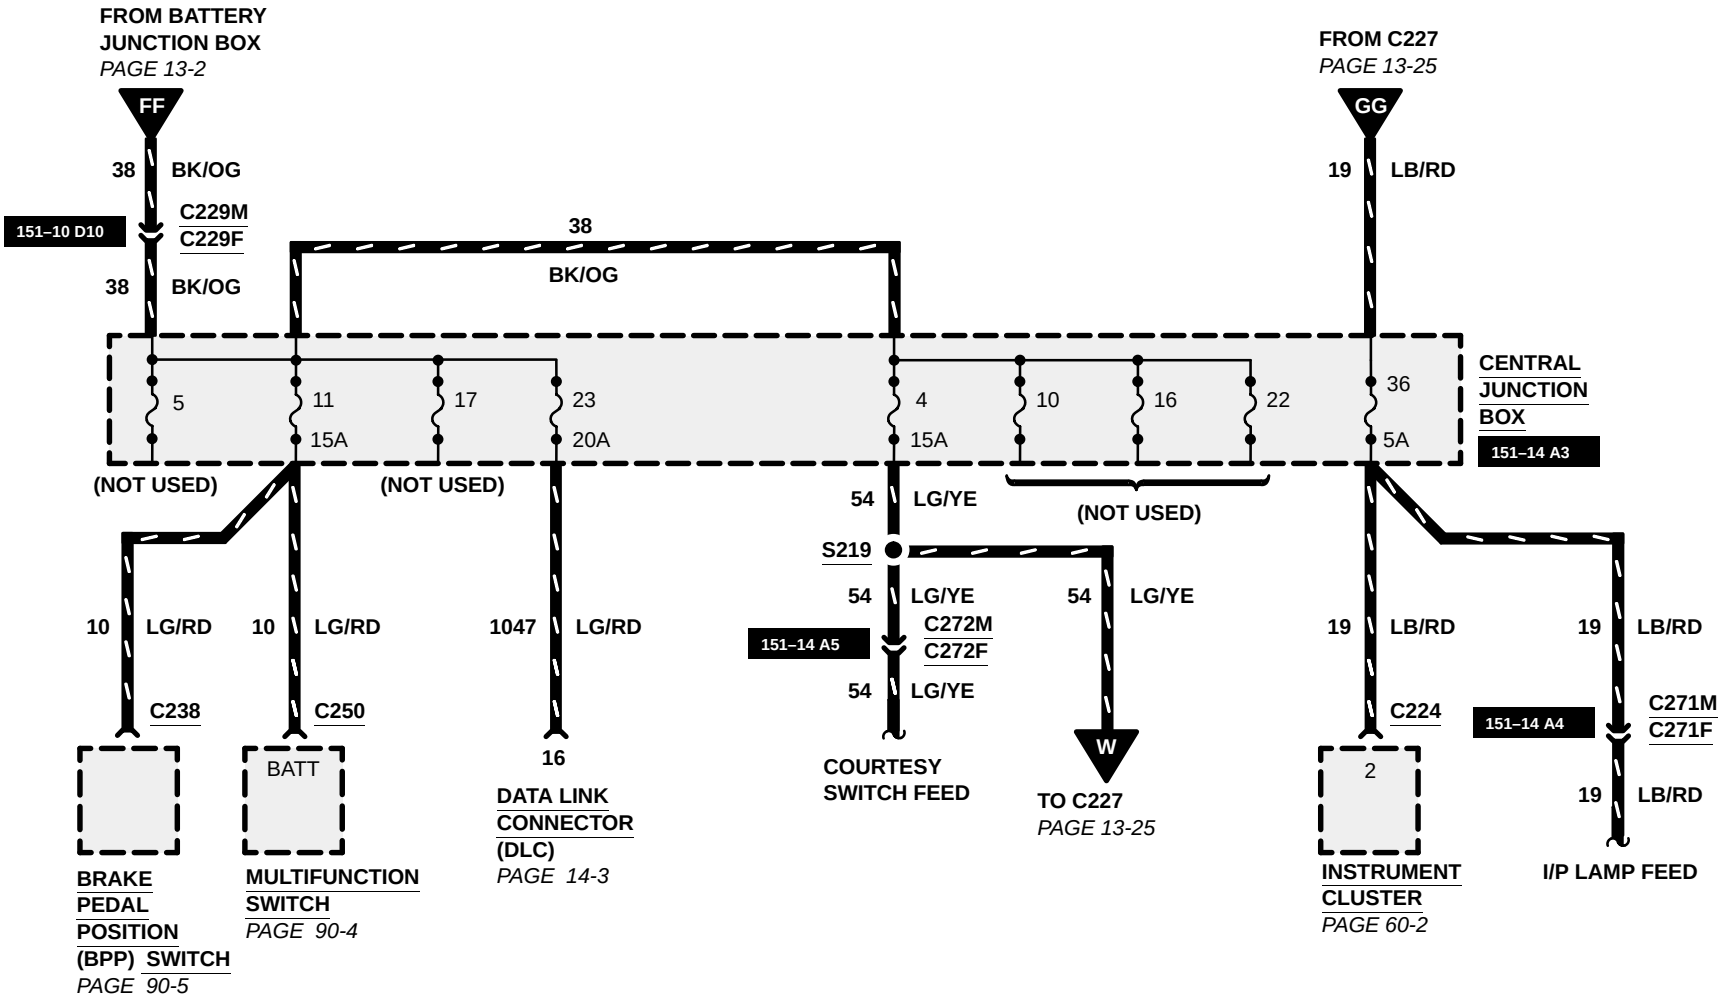
STRIPPED CHASSIS