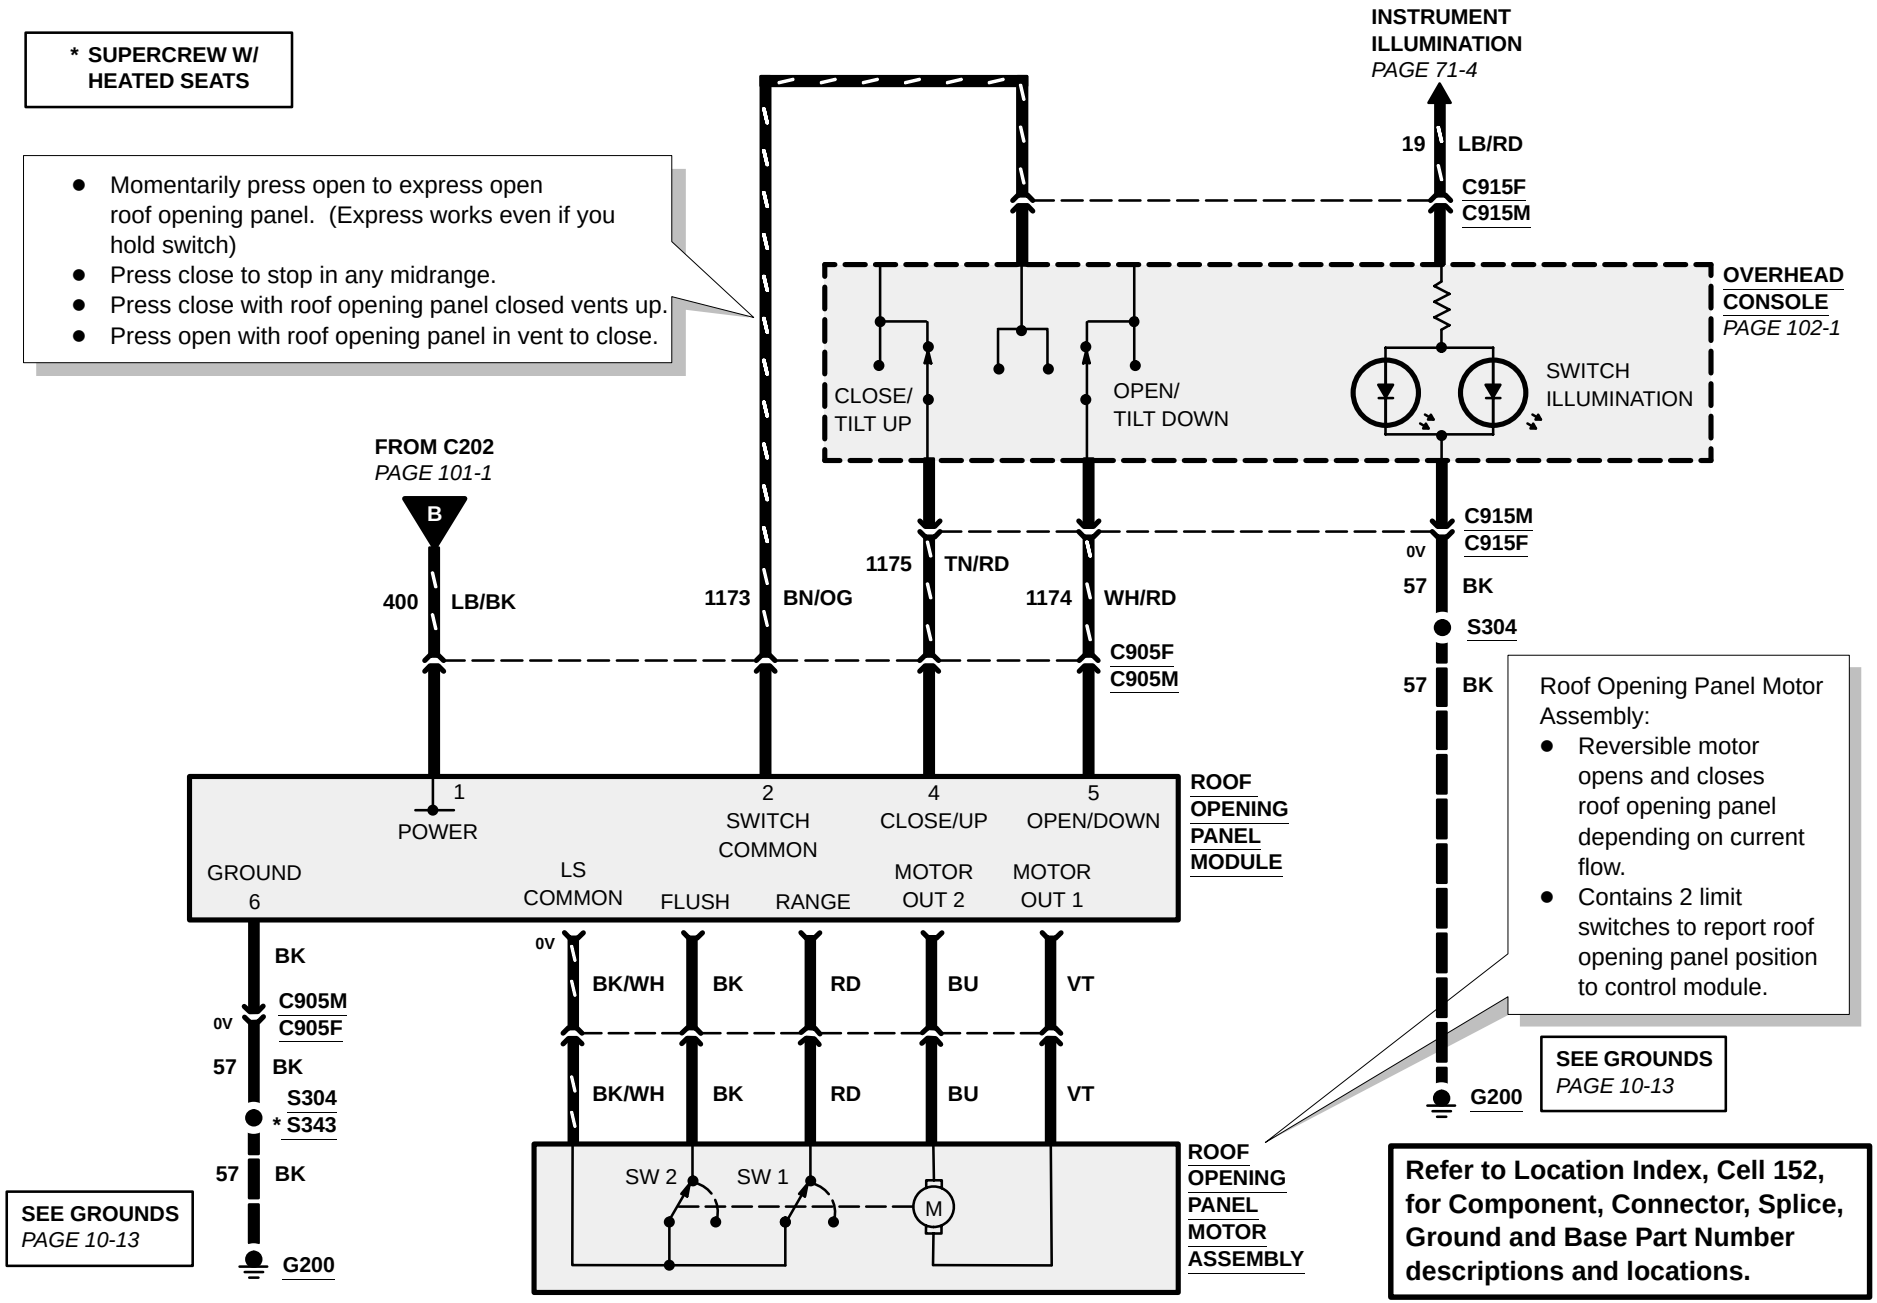ROOF OPENING PANEL 101-2