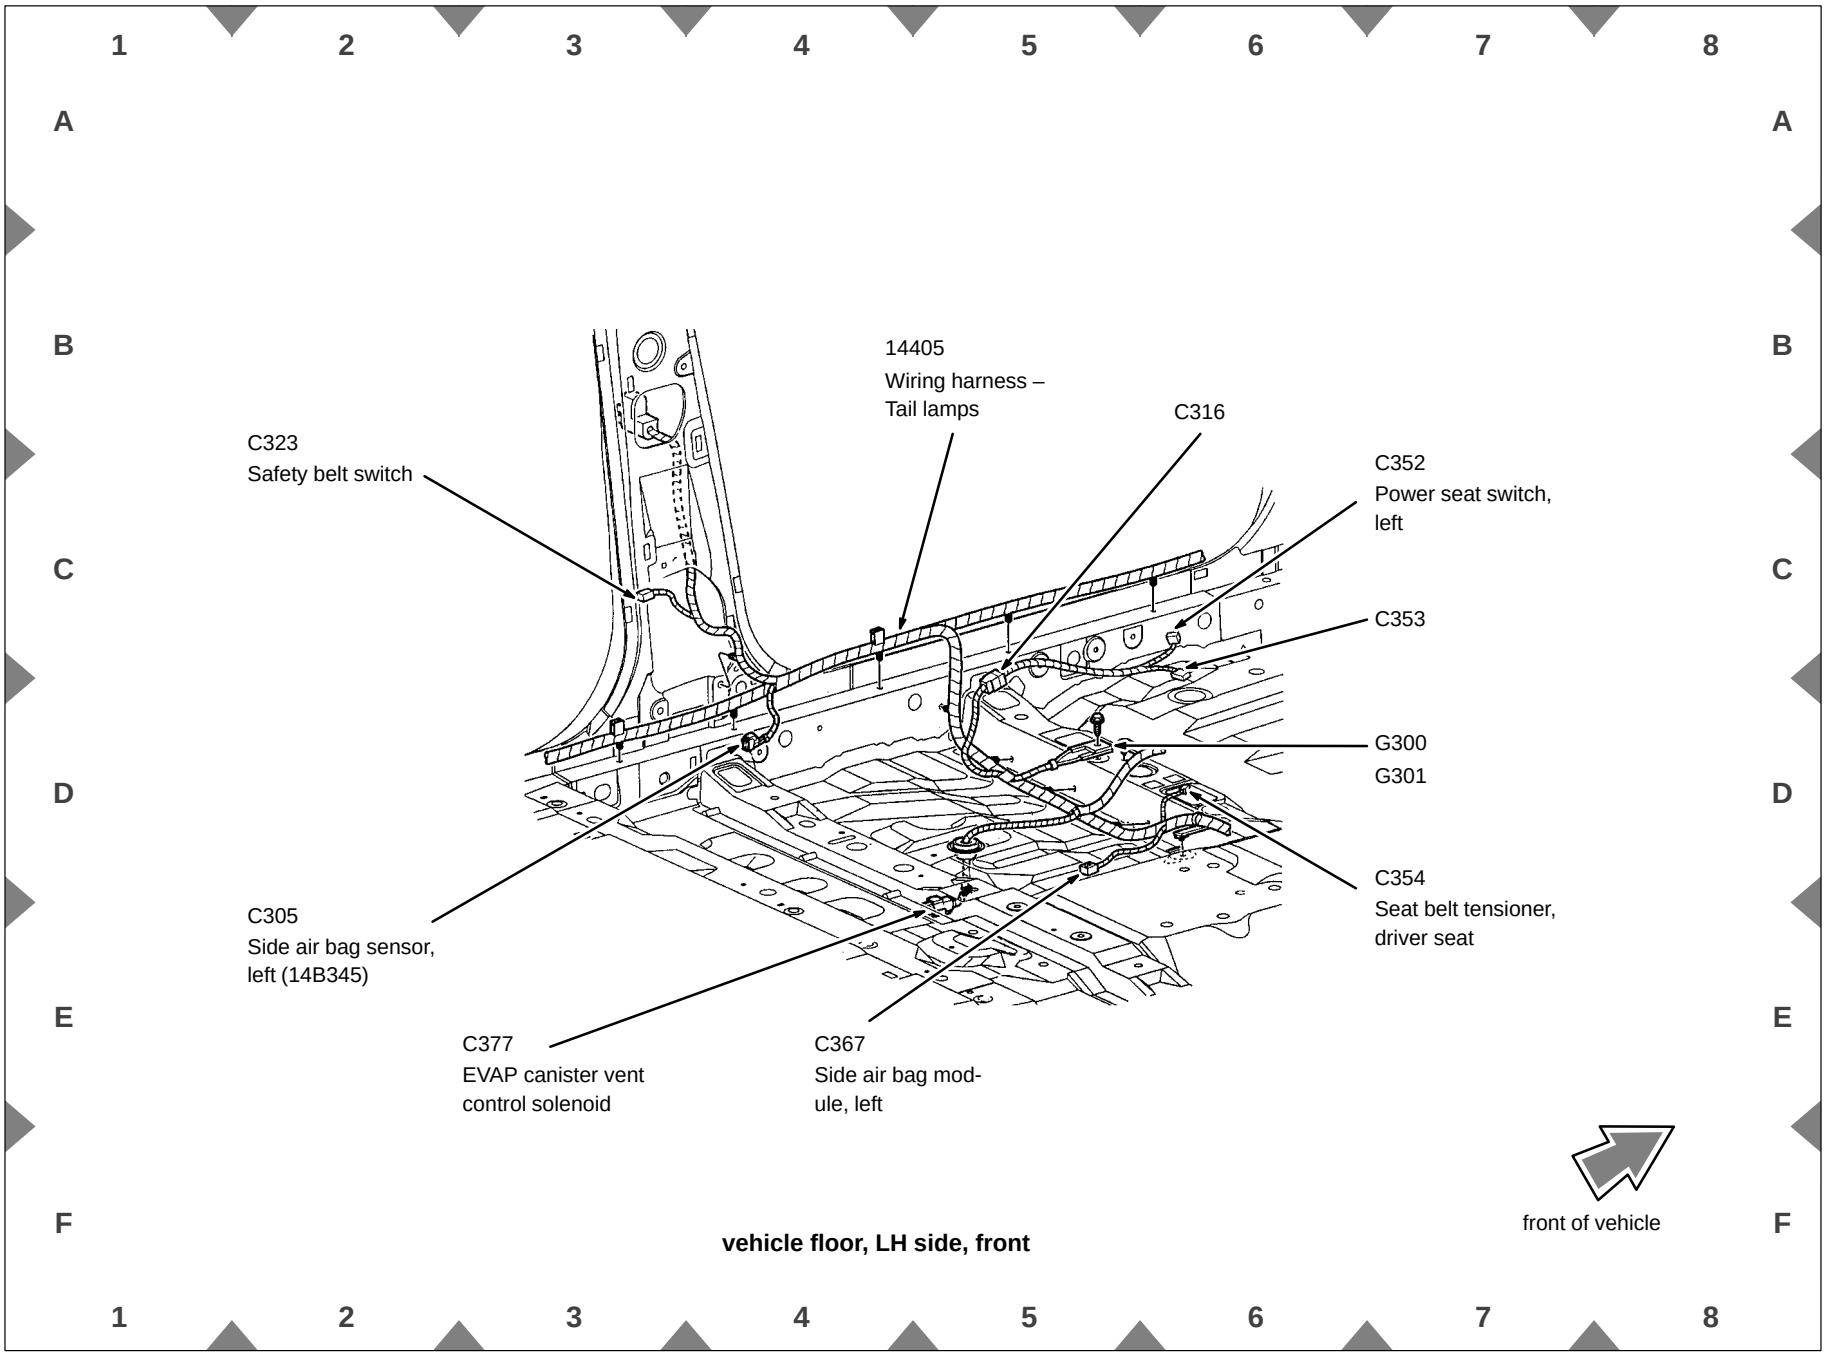

vehicle floor, LH side, front