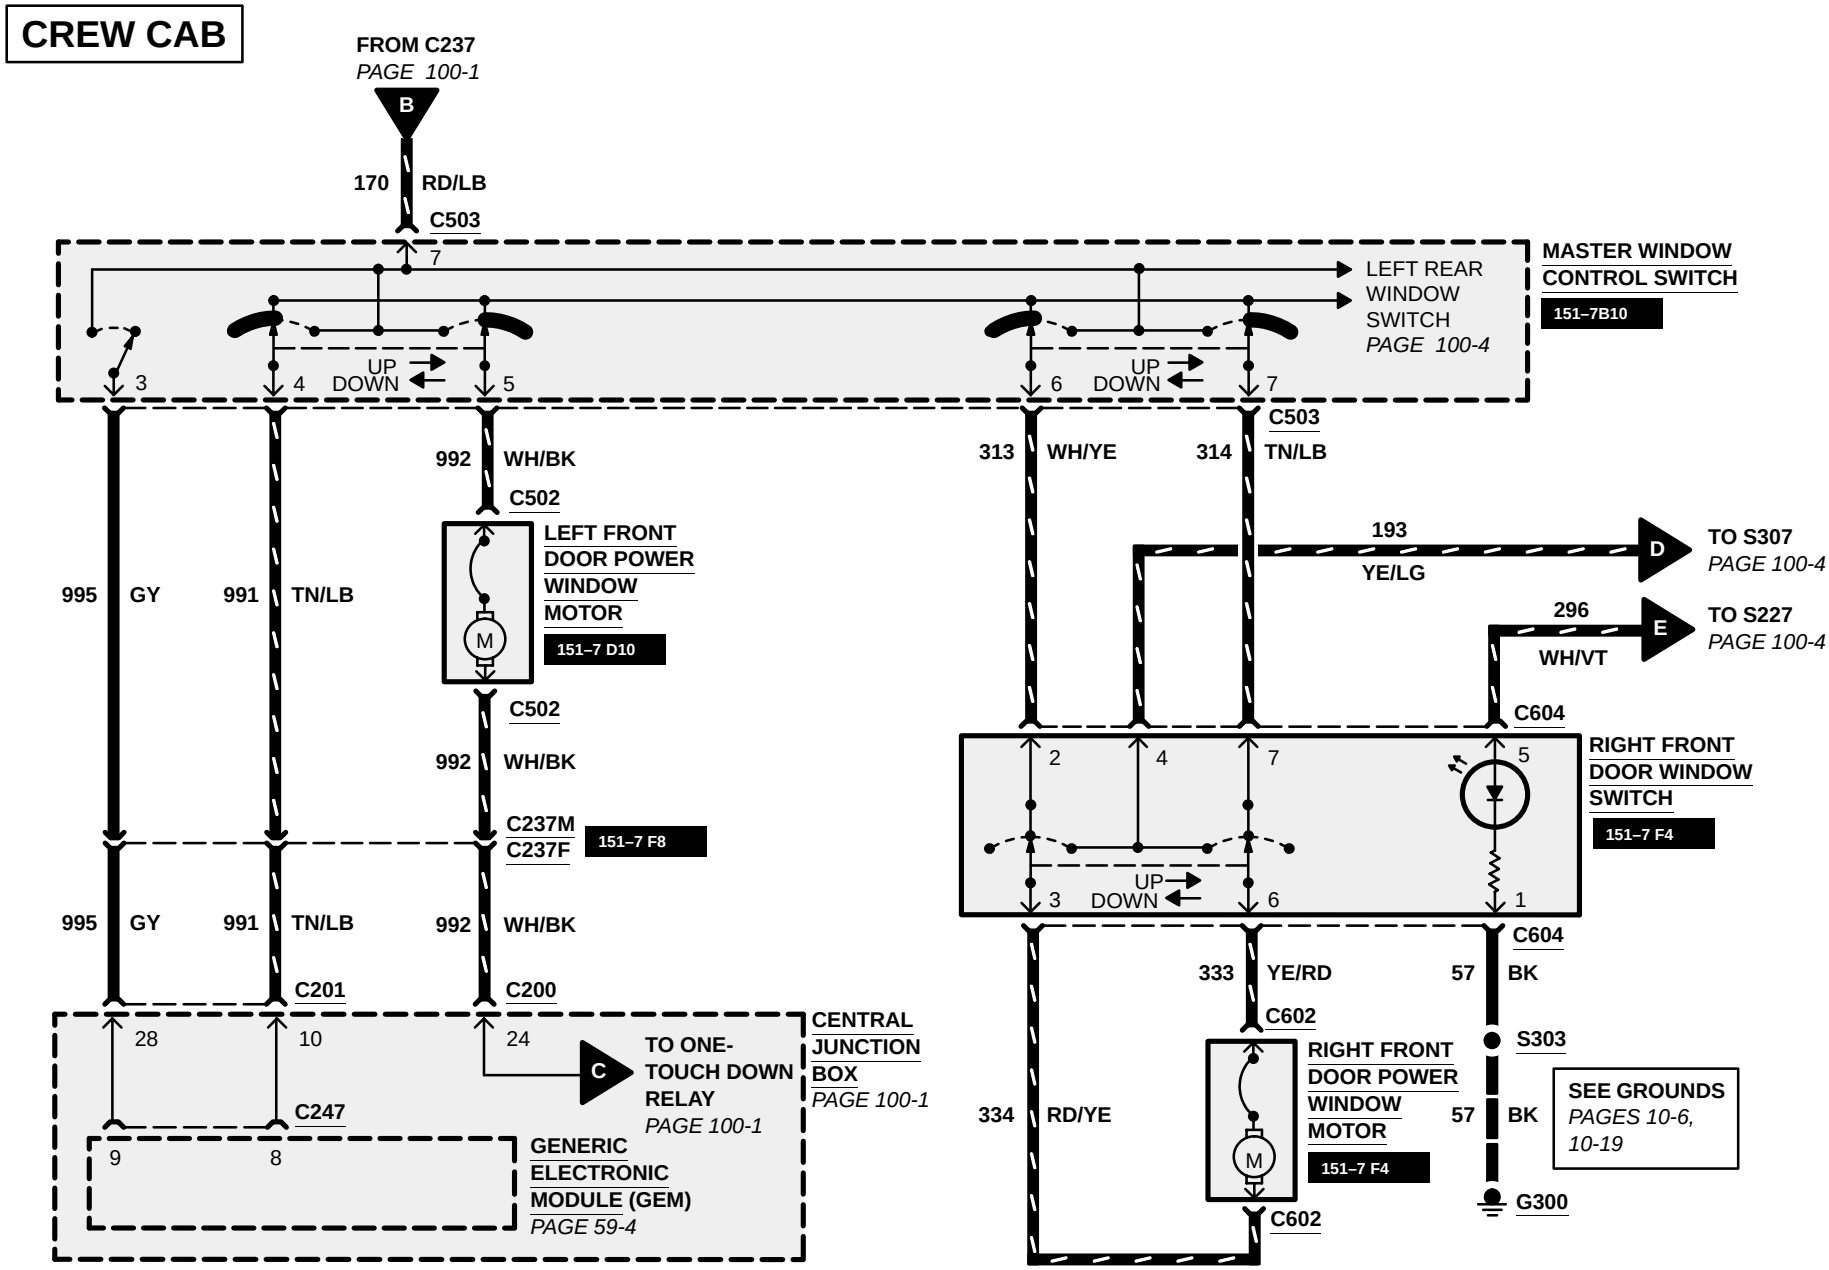100-3 POWER WINDOWS