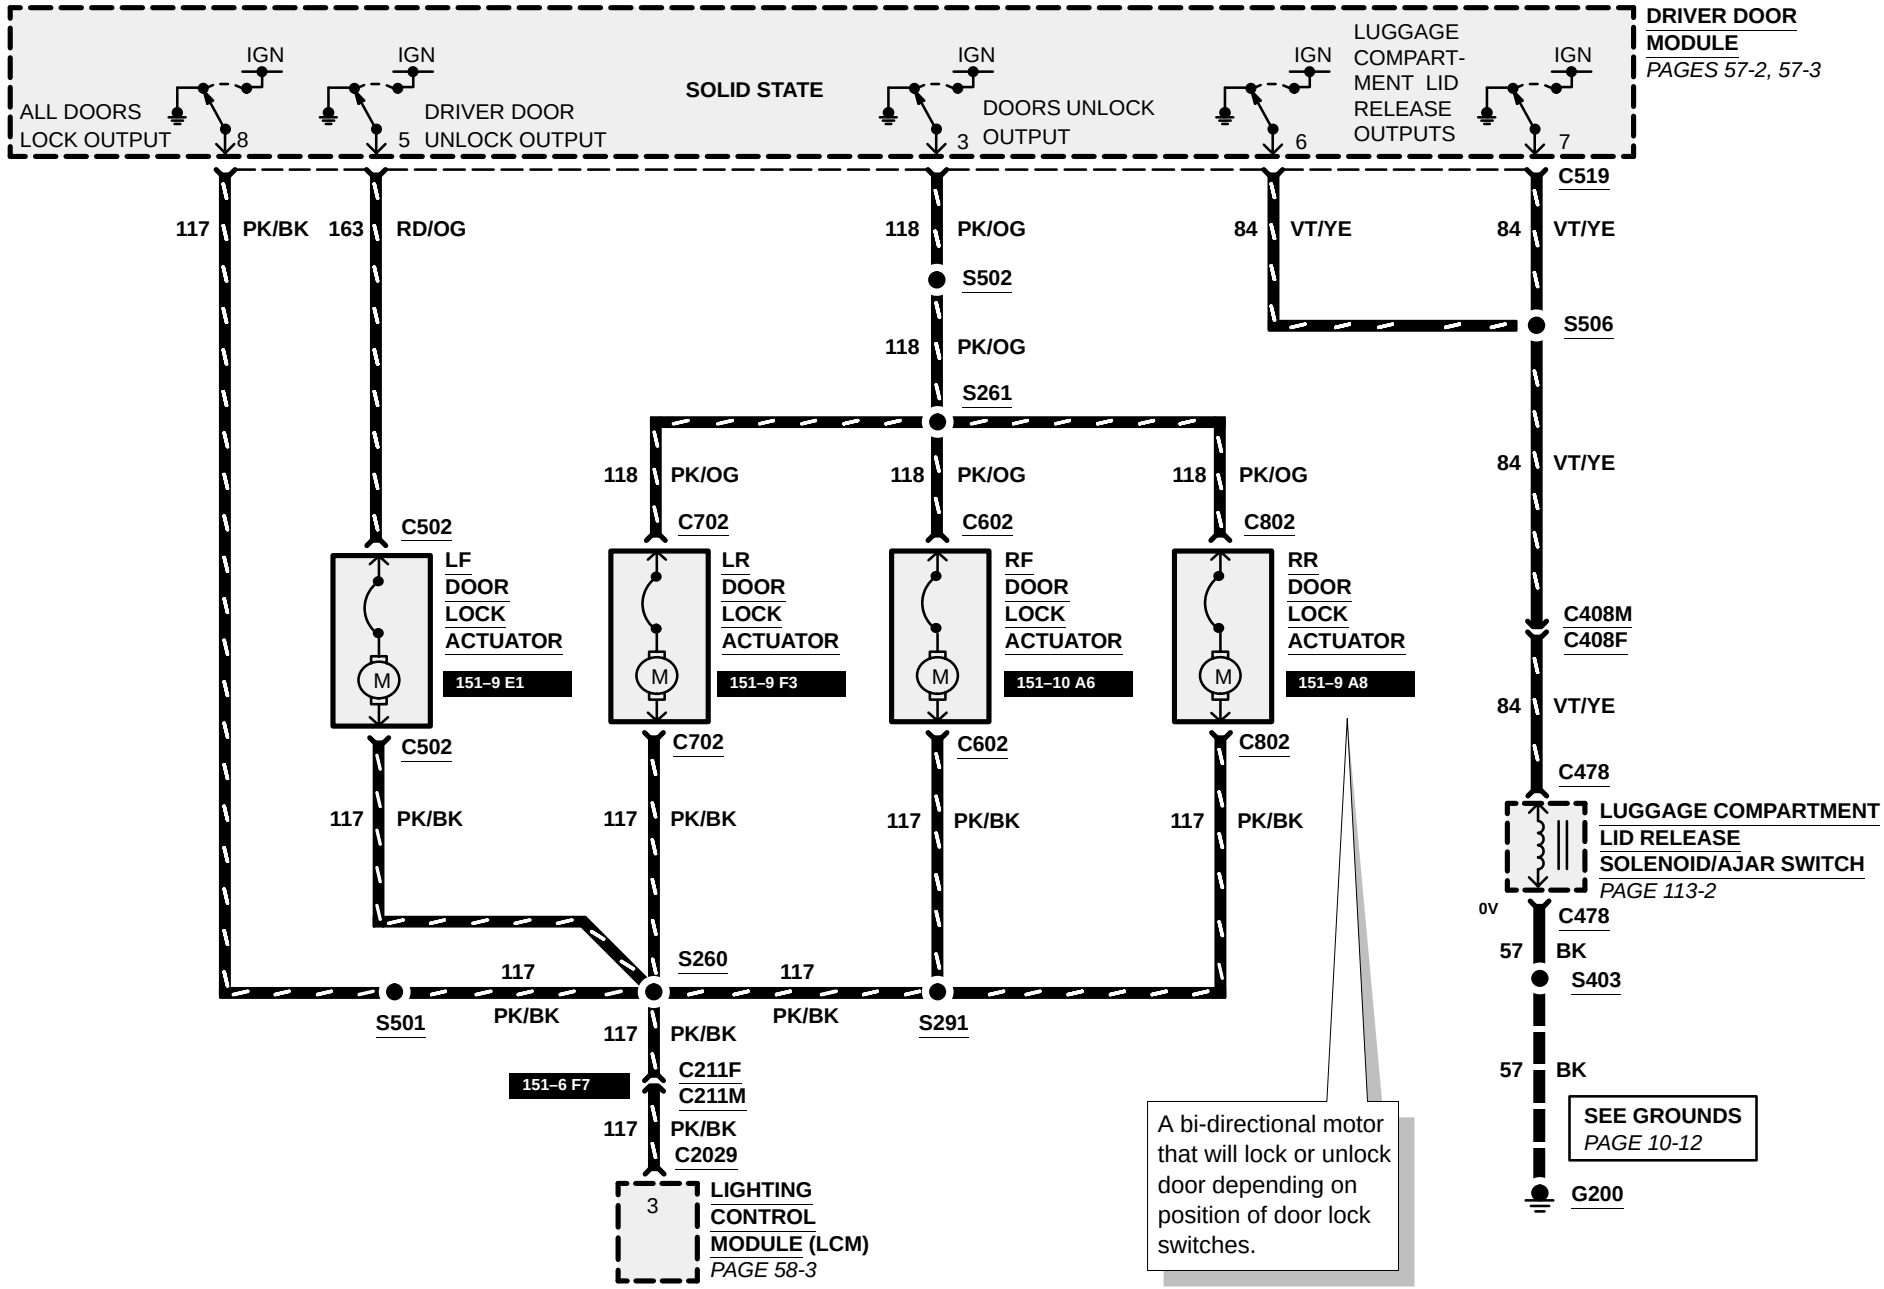# KEYLESS ENTRY (ILLUMINATED ENTRY) 111-2