For diagnostic information refer to Section 412-00 of the Workshop Manual.
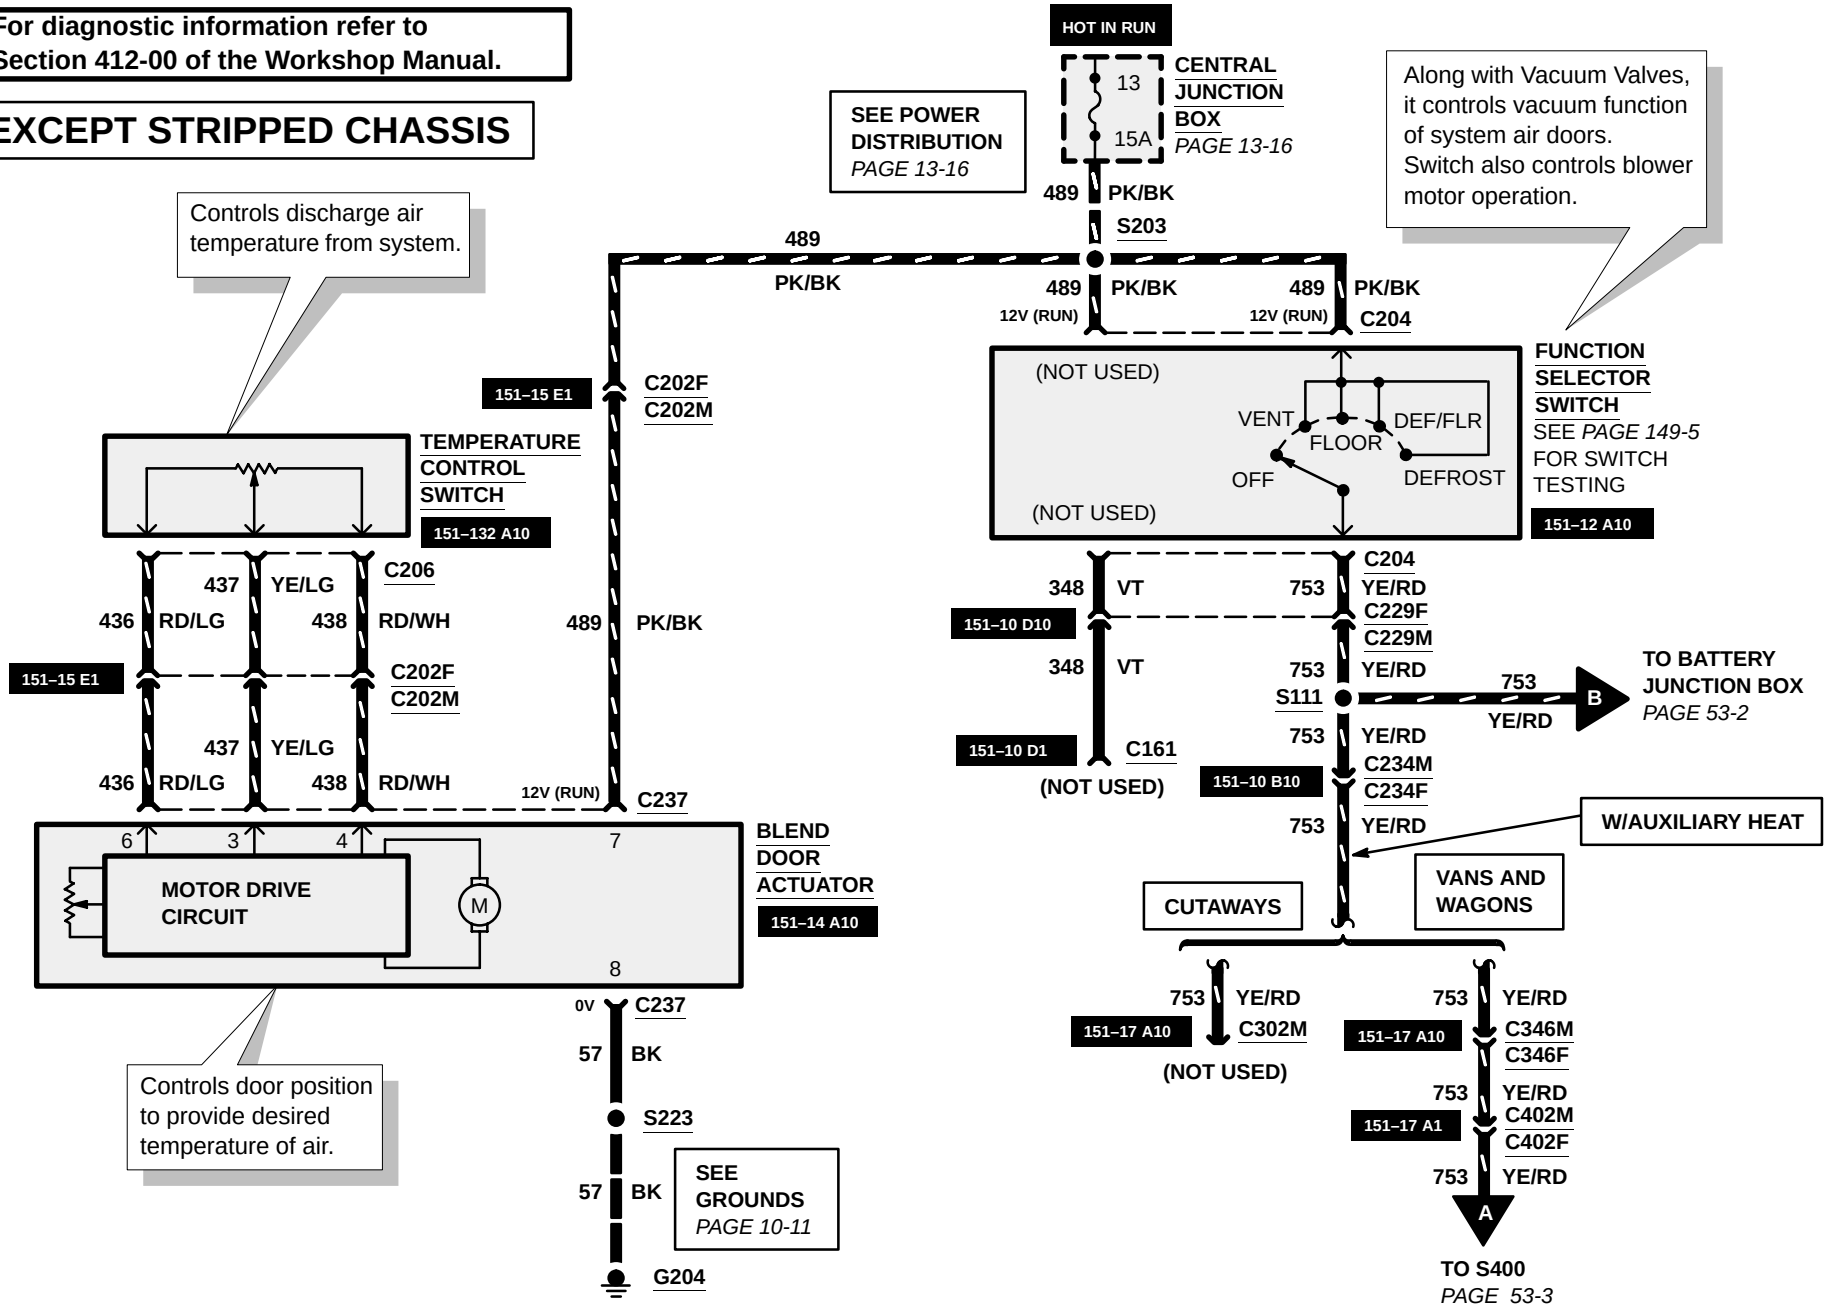
EXCEPT STRIPPED CHASSIS