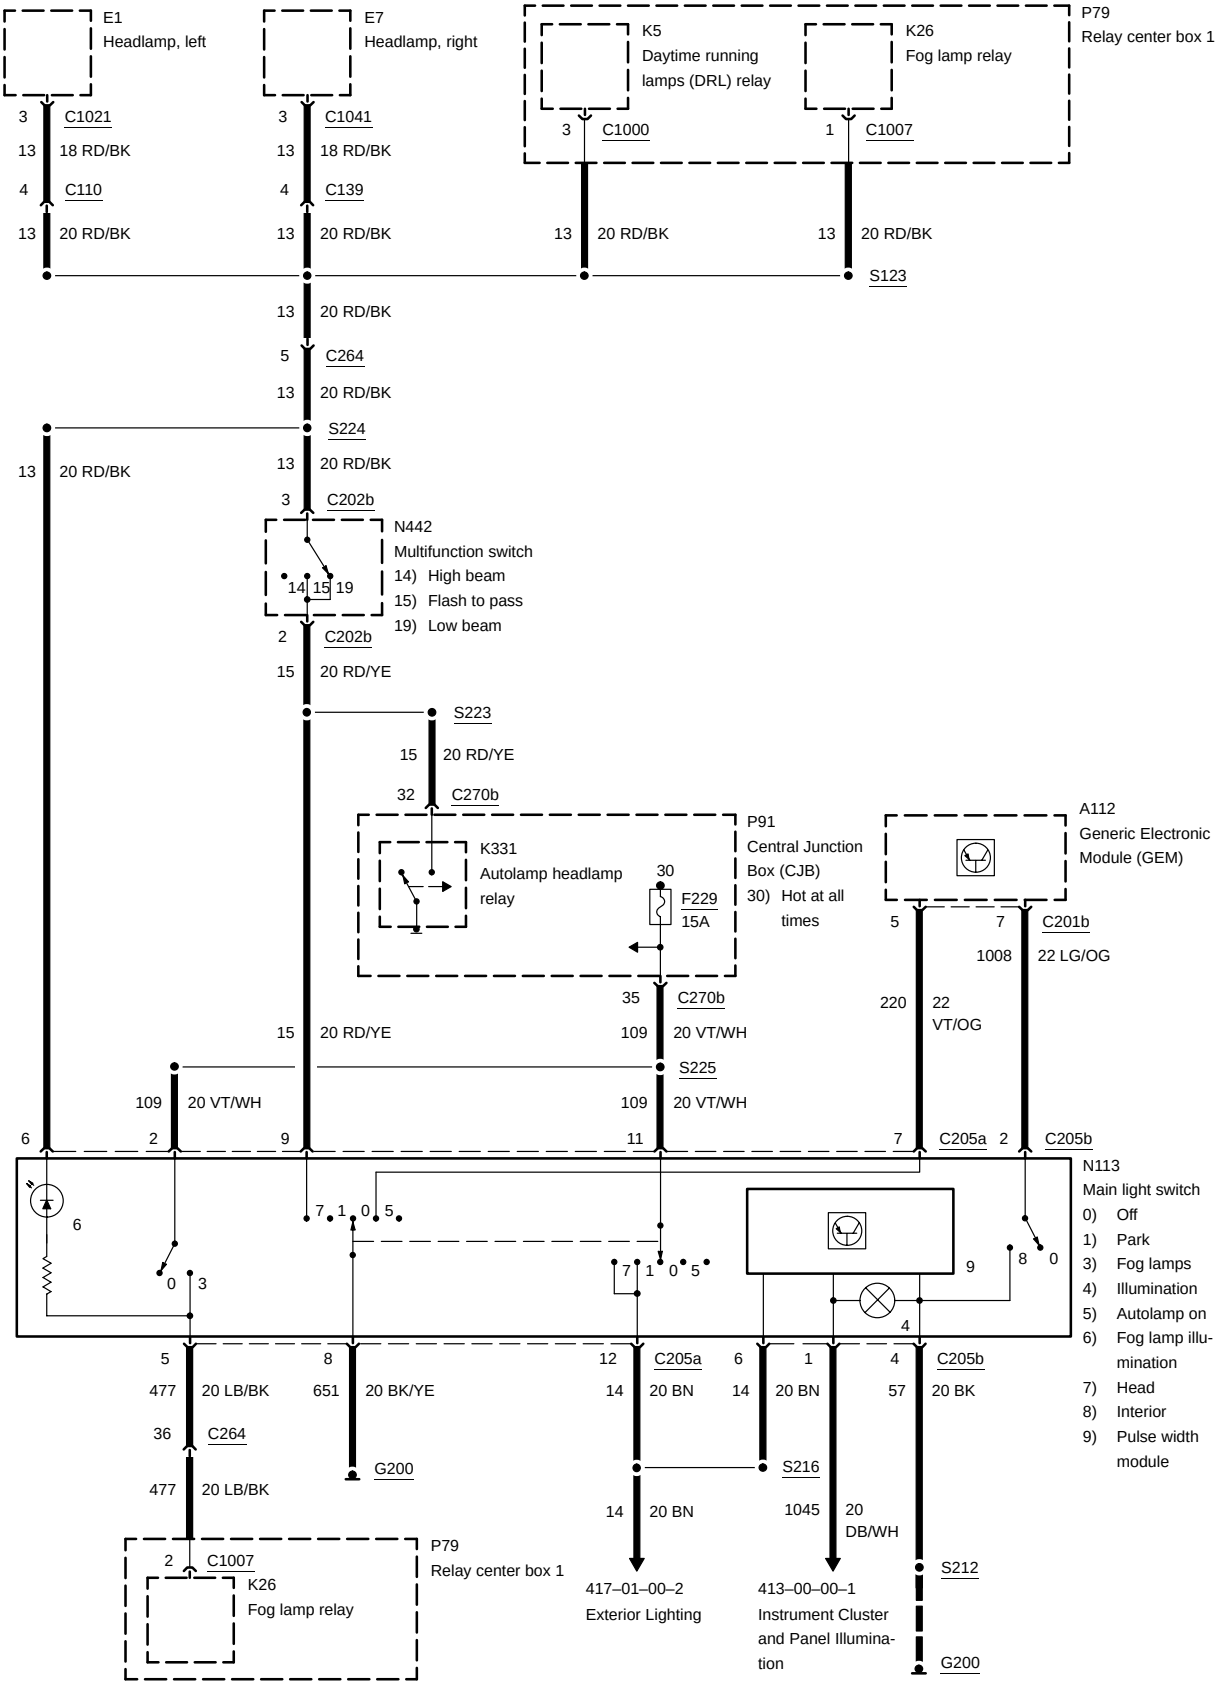Main light switch, with autolamps -10