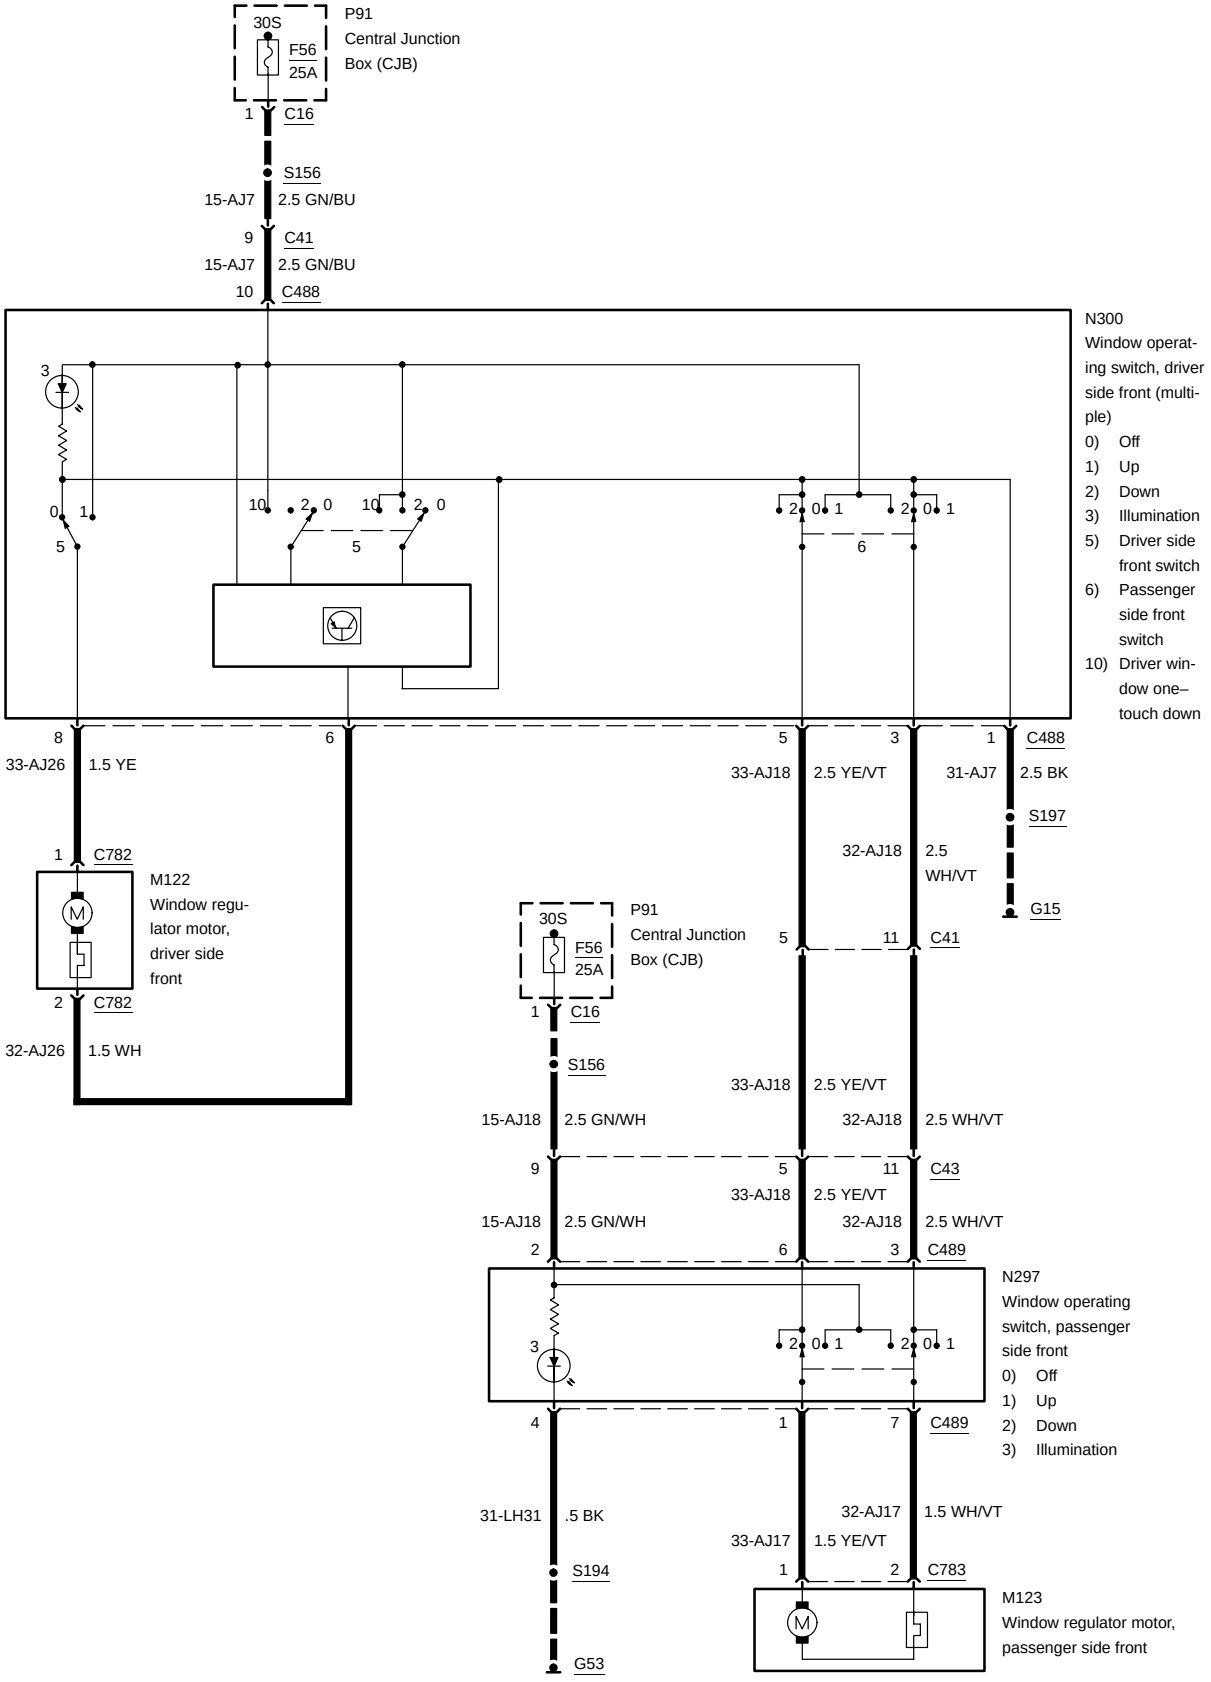with front power windows -1