SCHEMATIC

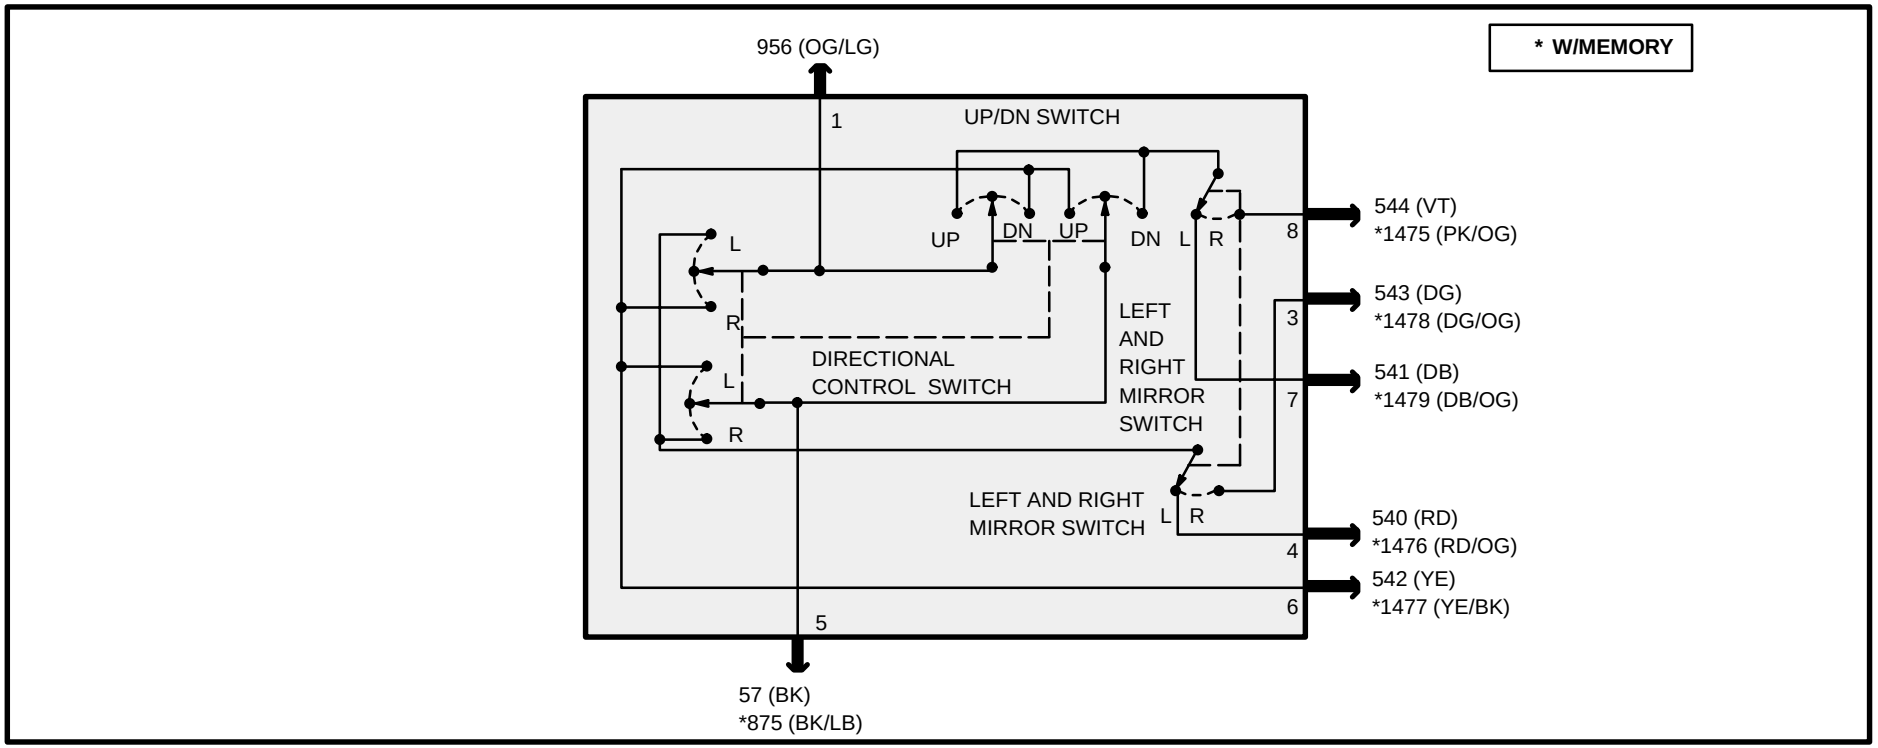

TERMINALS

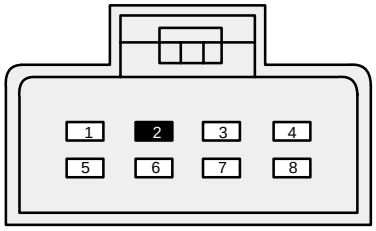

C511